OTVORY: šířka, spodní hrana (parapet), horní hrana, výšky od podlahy podlahy a absolutně (1NP, otvory-1NP.pdf)

otvor okna: spodní a horní hrana
dveře v rovném zdivu (v SDK ve nakresli, překlad tam není)
mezera ve zdivu bez výplně / bez kóty

## LEGENDA KONSTRUKCÍ - PŮDORYS

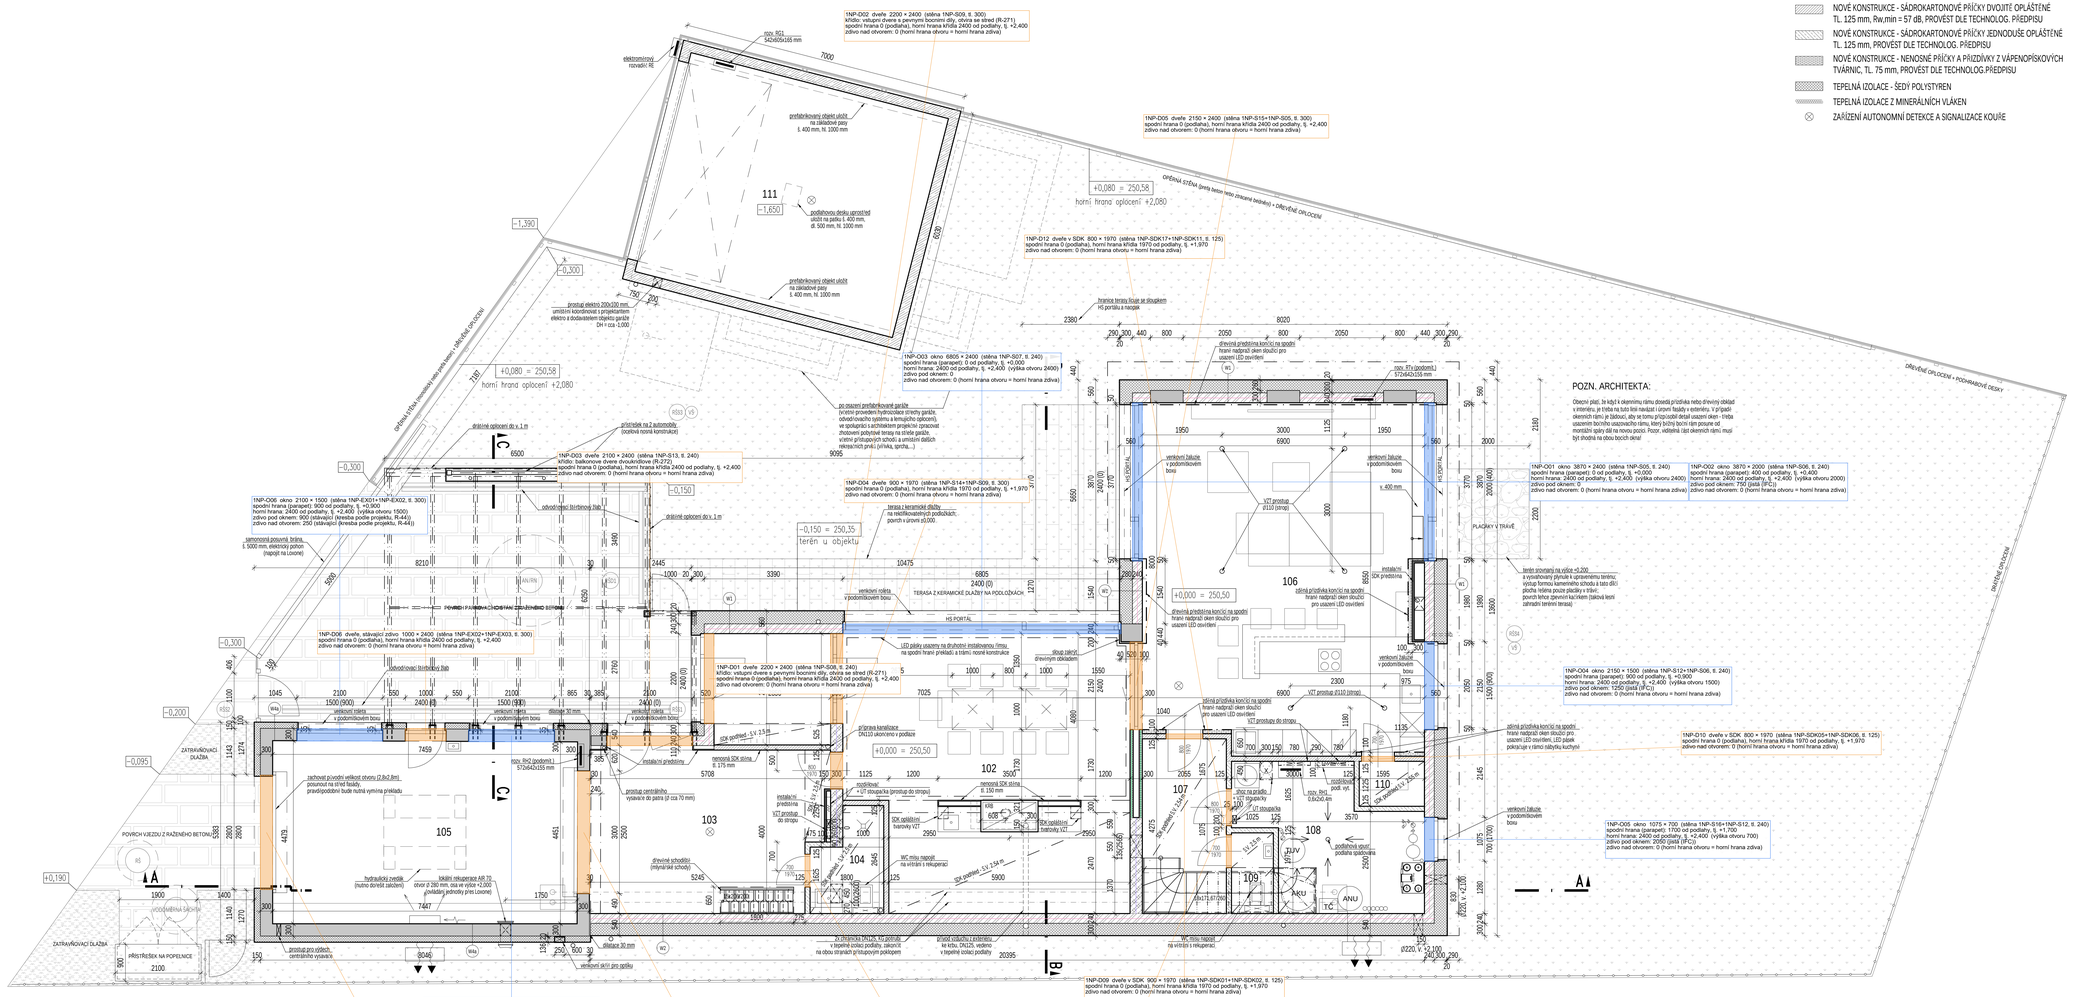
- STÁVAJÍCÍ KONSTRUKCE - SMÍŠENÉ ZDIVO (včetně omítky)
- NOVÉ KONSTRUKCE - ŽELEZOBETONOVÉ
- NOVÉ KONSTRUKCE - NOSNÉ ZDIVO Z VÁPENOPÍSKOVÝCH BLOKŮ VAPIS TL. 300 mm, PROVĚST DLE TECHNOLOG. PŘEDPISU
- NOVÉ KONSTRUKCE - NOSNÉ ZDIVO Z VÁPENOPÍSKOVÝCH BLOKŮ VAPIS TL. 240 mm, PROVĚST DLE TECHNOLOG. PŘEDPISU
- NOVÉ KONSTRUKCE - NOSNÉ ZDIVO Z VÁPENOPÍSKOVÝCH BLOKŮ VAPIS TL. 200 mm, PROVĚST DLE TECHNOLOG. PŘEDPISU
- NOVÉ KONSTRUKCE - SÁDROKARTONOVÉ PŘÍČKY DVOJITĚ OPLÁŠTĚNÉ TL. 125 mm, Rw,min = 57 dB, PROVĚST DLE TECHNOLOG. PŘEDPISU
- NOVÉ KONSTRUKCE - SÁDROKARTONOVÉ PŘÍČKY JEDNODUŠE OPLÁŠTĚNÉ TL. 125 mm, PROVĚST DLE TECHNOLOG. PŘEDPISU
- NOVÉ KONSTRUKCE - NENOSNÉ PŘÍČKY A PŘIZDÍVKY Z VÁPENOPÍSKOVÝCH TVÁRNIC, TL. 75 mm, PROVĚST DLE TECHNOLOG.PŘEDPISU
- TEPELNÁ IZOLACE - ŠEDÝ POLYSTYREN
- TEPELNÁ IZOLACE Z MINERÁLNÍCH VLÁKEN
- ZAŘÍZENÍ AUTONOMNÍ DETEKCE A SIGNALIZACE KOUŘE

## TABULKA MÍSTNOSTÍ

| č.m. | místnost | plocha (m2) | s.v. (m) | podlaha | stěny | strop |
|---|---|---|---|---|---|---|
| 101 | Vstupní prostor | 7,8 | 2,70 a 2,5 | dlažba | malba | beton, SDK + malba |
| 102 | Hala - jídelna | 43,6 | 2,70 a 2,54 | dlažba | malba/obkl. | beton, SDK + malba |
| 103 | Dílna | 22,5 | 2,70 | stěrka | malba | beton |
| 104 | Sprcha, WC | 3,9 | 2,50 | dlažba | malba/obkl. | SDK + malba |
| 105 | Garáž | 33,3 | 5,97 | stěrka | malba | beton |
| 106 | Obývací pokoj, kuchyně | 57,3 | 2,70 a 2,60 | dlažba | malba/obkl. | beton |
| 107 | Hala - schodiště | 8,8 | 2,54 | dlažba | malba | SDK + malba |
| 108 | Technická místnost | 13,1 | 2,70 | dlažba | malba | beton |
| 109 | WC | 2,0 | 1,50 - 2,50 | dlažba | malba/obkl. | SDK + malba |
| 110 | Spíž | 1,8 | 2,55 | dlažba | malba/obkl. | SDK + malba |
| | Celkem | 192,6 | | | | |
| 111 | Samostatná samonosná dvojgaráž | 36,0 | prefabrikovaná betonová kce 7x6,03x2,47m; dodáno vcelku | | | |

**POZN. ARCHITEKTA:**

Obecný platí, že kdy k okenímu rámu dosedá příčka nebo dřevěný obklad v interiéru, je třeba na tuto linii nadojít úzkými lištami fasády v exteriéru. V případě okenních rámů je žádoucí, aby se tomu přizpůsobil detail usazení oken - třeba usazením bochníku usazovacího rámu, který bočními lícemi posune od montážní spáry dál na novou pozici. Pozor, vzdálenál část okenních rámů musí být zhotovena na obou bocích okna!


1NP-D02 dveře 2200 × 2400 (stěna 1NP-S09, tl. 300)
křídlo: vstupní dveře s pevným bočním díly, otvírá se ven, (R-271)
spodní hrana 0 (podlaha), horní hrana křídla 2400 od podlahy, tj. +2,400
zdivo nad otvorem: 0 (horní hrana otvoru = horní hrana zdiva)
1NP-D05 dveře 2150 × 2400 (stěna 1NP-S15+1NP-S05, tl. 300)
spodní hrana 0 (podlaha), horní hrana křídla 2400 od podlahy, tj. +2,400
zdivo nad otvorem: 0 (horní hrana otvoru = horní hrana zdiva)
1NP-D12 dveře v SDK 800 × 1970 (stěna 1NP-SDK17+1NP-SDK11, tl. 125)
spodní hrana 0 (podlaha), horní hrana křídla 1970 od podlahy, tj. +1,970
zdivo nad otvorem: 0 (horní hrana otvoru = horní hrana zdiva)
1NP-O03 okno 6805 × 2400 (stěna 1NP-S07, tl. 240)
spodní hrana (parapet): 0 od podlahy, tj. +0,000
horní hrana: 2400 od podlahy, tj. +2,400 (výška otvoru 2400)
zdivo pod oknem: 0
zdivo nad otvorem: 0 (horní hrana otvoru = horní hrana zdiva)
1NP-D03 dveře 2100 × 2400 (stěna 1NP-S13, tl. 240)
křídlo: balkonové dveře dvoukřídlové (R-272)
spodní hrana 0 (podlaha), horní hrana křídla 2400 od podlahy, tj. +2,400
zdivo nad otvorem: 0 (horní hrana otvoru = horní hrana zdiva)
1NP-D04 dveře 800 × 1970 (stěna 1NP-S14+1NP-S09, tl. 300)
spodní hrana 0 (podlaha), horní hrana křídla 1970 od podlahy, tj. +1,970
zdivo nad otvorem: 0 (horní hrana otvoru = horní hrana zdiva)
1NP-O06 okno 2100 × 1500 (stěna 1NP-EX01+1NP-EX02, tl. 300)
spodní hrana (parapet): 900 od podlahy, tj. +0,900
horní hrana: 2400 od podlahy, tj. +2,400 (výška otvoru 1500)
zdivo pod oknem: 900 (stávající) /kreslba podle projektu, R-44/)
zdivo nad otvorem: 250 (stávající) /kreslba podle projektu, R-44/)
1NP-D06 dveře, stávající zdivo 1000 × 2400 (stěna 1NP-EX02+1NP-EX03, tl. 300)
spodní hrana 0 (podlaha), horní hrana křídla 2400 od podlahy, tj. +2,400
zdivo nad otvorem: 0 (horní hrana otvoru = horní hrana zdiva)
1NP-D01 dveře 2200 × 2400 (stěna 1NP-S08, tl. 240)
křídlo: vstupní dveře s pevným bočním díly, otvírá se ven, (R-271)
spodní hrana 0 (podlaha), horní hrana křídla 2400 od podlahy, tj. +2,400
zdivo nad otvorem: 0 (horní hrana otvoru = horní hrana zdiva)
1NP-O01 okno 3870 × 2400 (stěna 1NP-S05, tl. 240)
spodní hrana (parapet): 0 od podlahy, tj. +0,000
horní hrana: 2400 od podlahy, tj. +2,400 (výška otvoru 2400)
zdivo pod oknem: 0
zdivo nad otvorem: 0 (horní hrana otvoru = horní hrana zdiva)
1NP-O02 okno 3870 × 2000 (stěna 1NP-S06, tl. 240)
spodní hrana (parapet): 400 od podlahy, tj. +0,400
horní hrana: 2400 od podlahy, tj. +2,400 (výška otvoru 2000)
zdivo pod oknem: 790 (pásl (IFC))
zdivo nad otvorem: 0 (horní hrana otvoru = horní hrana zdiva)
1NP-O04 okno 2150 × 1500 (stěna 1NP-S12+1NP-S06, tl. 240)
spodní hrana (parapet): 900 od podlahy, tj. +0,900
horní hrana: 2400 od podlahy, tj. +2,400 (výška otvoru 1500)
zdivo pod oknem: 1250 (pásl (IFC))
zdivo nad otvorem: 0 (horní hrana otvoru = horní hrana zdiva)
1NP-D10 dveře v SDK 800 × 1970 (stěna 1NP-SDK04+1NP-SDK08, tl. 125)
spodní hrana 0 (podlaha), horní hrana křídla 1970 od podlahy, tj. +1,970
zdivo nad otvorem: 0 (horní hrana otvoru = horní hrana zdiva)
1NP-O05 okno 1075 × 700 (stěna 1NP-S16+1NP-S12, tl. 240)
spodní hrana (parapet): 1700 od podlahy, tj. +1,700
horní hrana: 2400 od podlahy, tj. +2,400 (výška otvoru 700)
zdivo pod oknem: 2050 (pásl (IFC))
zdivo nad otvorem: 0 (horní hrana otvoru = horní hrana zdiva)
1NP-D09 dveře v SDK 900 × 1970 (stěna 1NP-SDK01+1NP-SDK02, tl. 125)
spodní hrana 0 (podlaha), horní hrana křídla 1970 od podlahy, tj. +1,970
zdivo nad otvorem: 0 (horní hrana otvoru = horní hrana zdiva)
1NP-O07 okno 2100 × 1500 (stěna 1NP-EX03+1NP-EX04, tl. 300)
spodní hrana (parapet): 900 od podlahy, tj. +0,900
horní hrana: 2400 od podlahy, tj. +2,400 (výška otvoru 1500)
zdivo pod oknem: 900 (stávající) /kreslba podle projektu, R-44/)
zdivo nad otvorem: 250 (stávající) /kreslba podle projektu, R-44/)
1NP-D07 dveře, stávající zdivo 2800 × 2800 (stěna 1NP-EX07+1NP-EX08, tl. 300)
spodní hrana 0 (podlaha), horní hrana křídla 2800 od podlahy, tj. +2,800
zdivo nad otvorem: 0 (horní hrana otvoru = horní hrana zdiva)
1NP-D08 dveře, stávající zdivo 3000 × 2500 (stěna 1NP-EX08+1NP-EX05, tl. 300)
spodní hrana 0 (podlaha), horní hrana křídla 2500 od podlahy, tj. +2,500
zdivo nad otvorem: 0 (horní hrana otvoru = horní hrana zdiva)
1NP-D13 dveře v SDK 800 × 1970 (stěna 1NP-SDK19+1NP-SDK14, tl. 125)
spodní hrana 0 (podlaha), horní hrana křídla 1970 od podlahy, tj. +1,970
zdivo nad otvorem: 0 (horní hrana otvoru = horní hrana zdiva)
1NP-D11 dveře v SDK 900 × 1970 (stěna 1NP-SDK11+1NP-SDK07, tl. 125)
spodní hrana 0 (podlaha), horní hrana křídla 1970 od podlahy, tj. +1,970
zdivo nad otvorem: 0 (horní hrana otvoru = horní hrana zdiva)
+0,080 = 250,58
horní hrana oplocení +2,080
−0,150 = 250,35
terén u objektu
+0,000 = 250,50
−0,300
−0,150
−0,200
−0,095
+0,190
−1,390
−1,650
111
105
106
107
108
109
110
102
103
104
ZATRAVŇOVACÍ DLAŽBA
PŘÍSTŘEŠEK NA POPELNICE
VODOMĚRNÁ ŠACHTA
POVRCH VJEZDU Z RAŽENÉHO BETONU
PŘÍPOJNÉ MÍSTO PRO ELEKTRO
TERÉNNÍ ÚPRAVY
PLACHTY V TRÁVĚ
OPLOCENÍ
OPĚRNÁ STĚNA GABIONŮ
OPĚRNÁ STĚNA gabiony betonu
OŘEZÁVKA
ODVODNĚNÍ
ANU
AKU
TC
RS
VS
HS PORTÁL
TERASA Z KERAMICKÉ DLAŽBY NA PODLOŽKÁCH
LED pásky uloženy na druhotně instalovanou římsu na spodní hraně překladu a trámů nosné konstrukce
VCT prostup Ø110 (strop)
VCT prostup Ø110 (podlaha)
nerezová SDK stříška tl. 175 mm
nerezová SDK stříška tl. 150 mm
SDK opláštění hatrovky VZT
SDK opláštění hatrovky VZT
SDK opláštění hatrovky VZT