
Barva osy = tloušťka zdiva, Porotherm 30 podle materiálu

- VAPIS 300 mm
- VAPIS 240 mm
- VAPIS 200 mm
- VPC 75 mm
- Porotherm 30 (nástavba garáže, R-87; ve výkrese VAPIS 300)

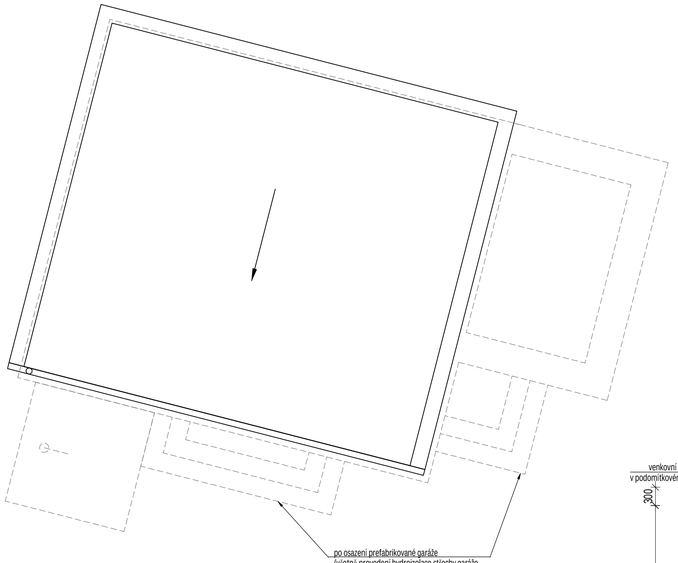


LEGENDA KONSTRUKCÍ - PŮDORYS

- STÁVAJÍCÍ KONSTRUKCE - SMÍŠENÉ ZDIVO (včetně omítky)
- NOVÉ KONSTRUKCE - ŽELEZOBETONOVÉ
- NOVÉ KONSTRUKCE - NOSNÉ ZDIVO Z VÁPENOPÍSKOVÝCH BLOKŮ VAPIS TL. 300 mm, PROVÉST DLE TECHNOLOG. PŘEDPISU
- NOVÉ KONSTRUKCE - NOSNÉ ZDIVO Z VÁPENOPÍSKOVÝCH BLOKŮ VAPIS TL. 240 mm, PROVÉST DLE TECHNOLOG. PŘEDPISU
- NOVÉ KONSTRUKCE - NOSNÉ ZDIVO Z VÁPENOPÍSKOVÝCH BLOKŮ VAPIS TL. 200 mm, PROVÉST DLE TECHNOLOG. PŘEDPISU
- NOVÉ KONSTRUKCE - SÁDROKARTONOVÉ PŘÍČKY DVOJITĚ OPLÁŠTĚNÉ TL. 125 mm, Rw,min = 57 dB, PROVÉST DLE TECHNOLOG. PŘEDPISU
- NOVÉ KONSTRUKCE - SÁDROKARTONOVÉ PŘÍČKY JEDNODUŠE OPLÁŠTĚNÉ TL. 125 mm, PROVÉST DLE TECHNOLOG. PŘEDPISU
- NOVÉ KONSTRUKCE - NENOSNÉ PŘÍČKY A PŘIZDÍVKY Z VÁPENOPÍSKOVÝCH TVÁRNIC, TL. 75 mm, PROVÉST DLE TECHNOLOG.PŘEDPISU
- TEPELNÁ IZOLACE - ŠEDÝ POLYSTYREN
- TEPELNÁ IZOLACE Z MINERÁLNÍCH VLÁKEN
- ZAŘÍZENÍ AUTONOMNÍ DETEKCE A SIGNALIZACE KOUŘE

TABULKA MÍSTNOSTÍ

č.m.	místnost	plocha (m2)	s.v. (m)	podlaha	stěny	strop
201	Hala	17,5	2,60	dlažba	malba	SDK + malba
202	Koupelna, WC	5,2	2,60	dlažba	malba/obkl.	SDK + malba
203	Šatna	11,1	2,60	dlažba	malba	SDK + malba
204	Koupelna, WC	5,5	2,60	dlažba	malba/obkl.	SDK + malba
205	Ložnice	14,1	2,70	dlažba	malba	SDK + malba
206	Ložnice	13,7	2,70	dlažba	malba	SDK + malba
207	Ložnice	15,6	2,70	dlažba	malba	SDK + malba
208	Pracovna	24,1	2,70	dlažba	malba	SDK + malba
209	Sklad, pracovna	23,2	2,70	dlažba	malba	SDK + malba
	Celkem	115,0				
210	Pobytová část střechy - terasa	22,7				
211	Nepochozí část střechy	26,0				

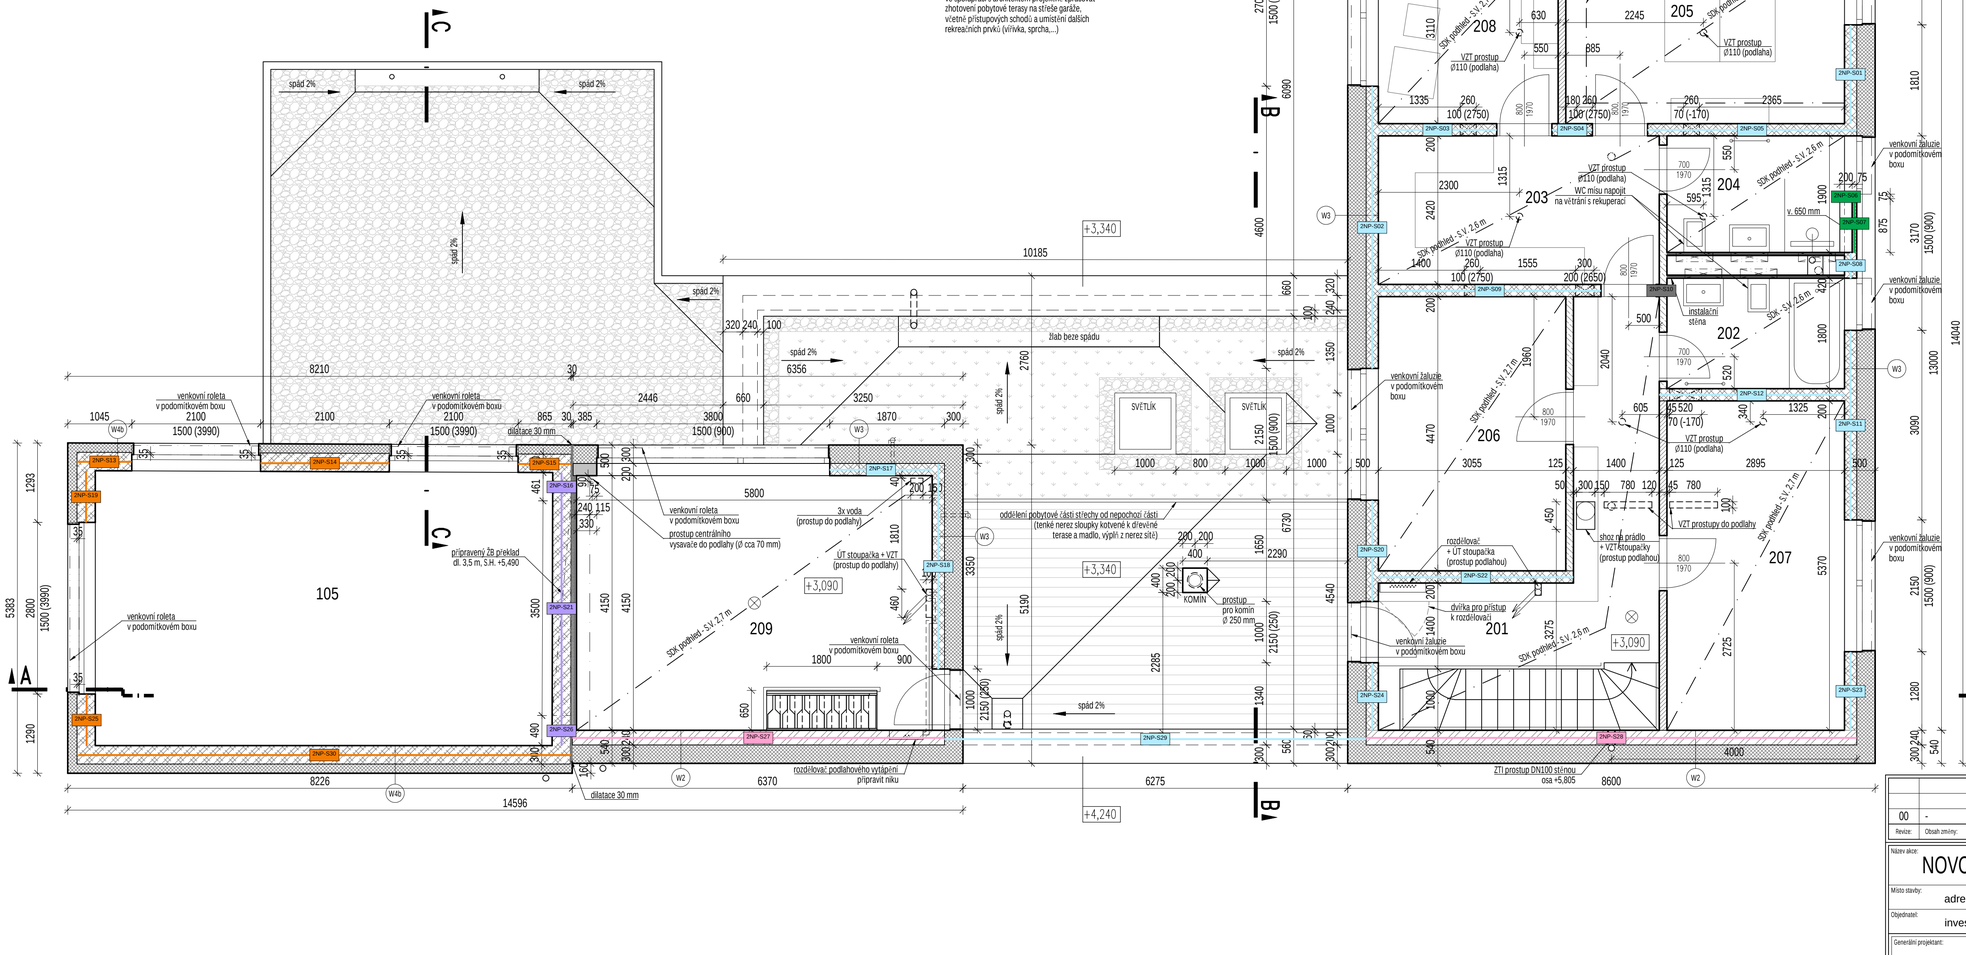

00	-	-	-
Revize:	Obsah změny:	Autor:	Datum:

Název akce: **NOVOSTAVBA RODINNÉHO DOMU**

Parié:

Místo stavby: adresa stavby neuvedena

Objednatel: investor

Generální projektant:

Profese:

Projektant: projektantka

Projekční tým: projektantka

Kontroloval:

Autorizační razítko:

Formát: -

Měřítko: 1:50

Část: ARCHITEKTONICKO - STAVEBNÍ

Číslo projektu:

Datum: 09/2026

Stupeň: -

Vydal: projektantka

Obsah výkresu: **PŮDORYS 2.NP**

Číslo výkresu: **D11-02**

DOKUMENTACE JE DUSEVNÍM MAJETKEM FIRMY RECOC S.R.O. A NESMÍ BÝT POUŽITA BEZ JEJÍHO VEDOMÍ