OTVORY: šířka, spodní hrana (parapet), horní hrana; výšky od podlahy podlaží a absolutně (1NP, otvory-1NP.pdf)

- 🟦 otvor okna: spodní a horní hrana
- 🟧 dveře v nosném zdivu (v SDK se nekreslí, překlad tam není)
- ⬜ mezera ve zdivu bez výplně / bez kóty

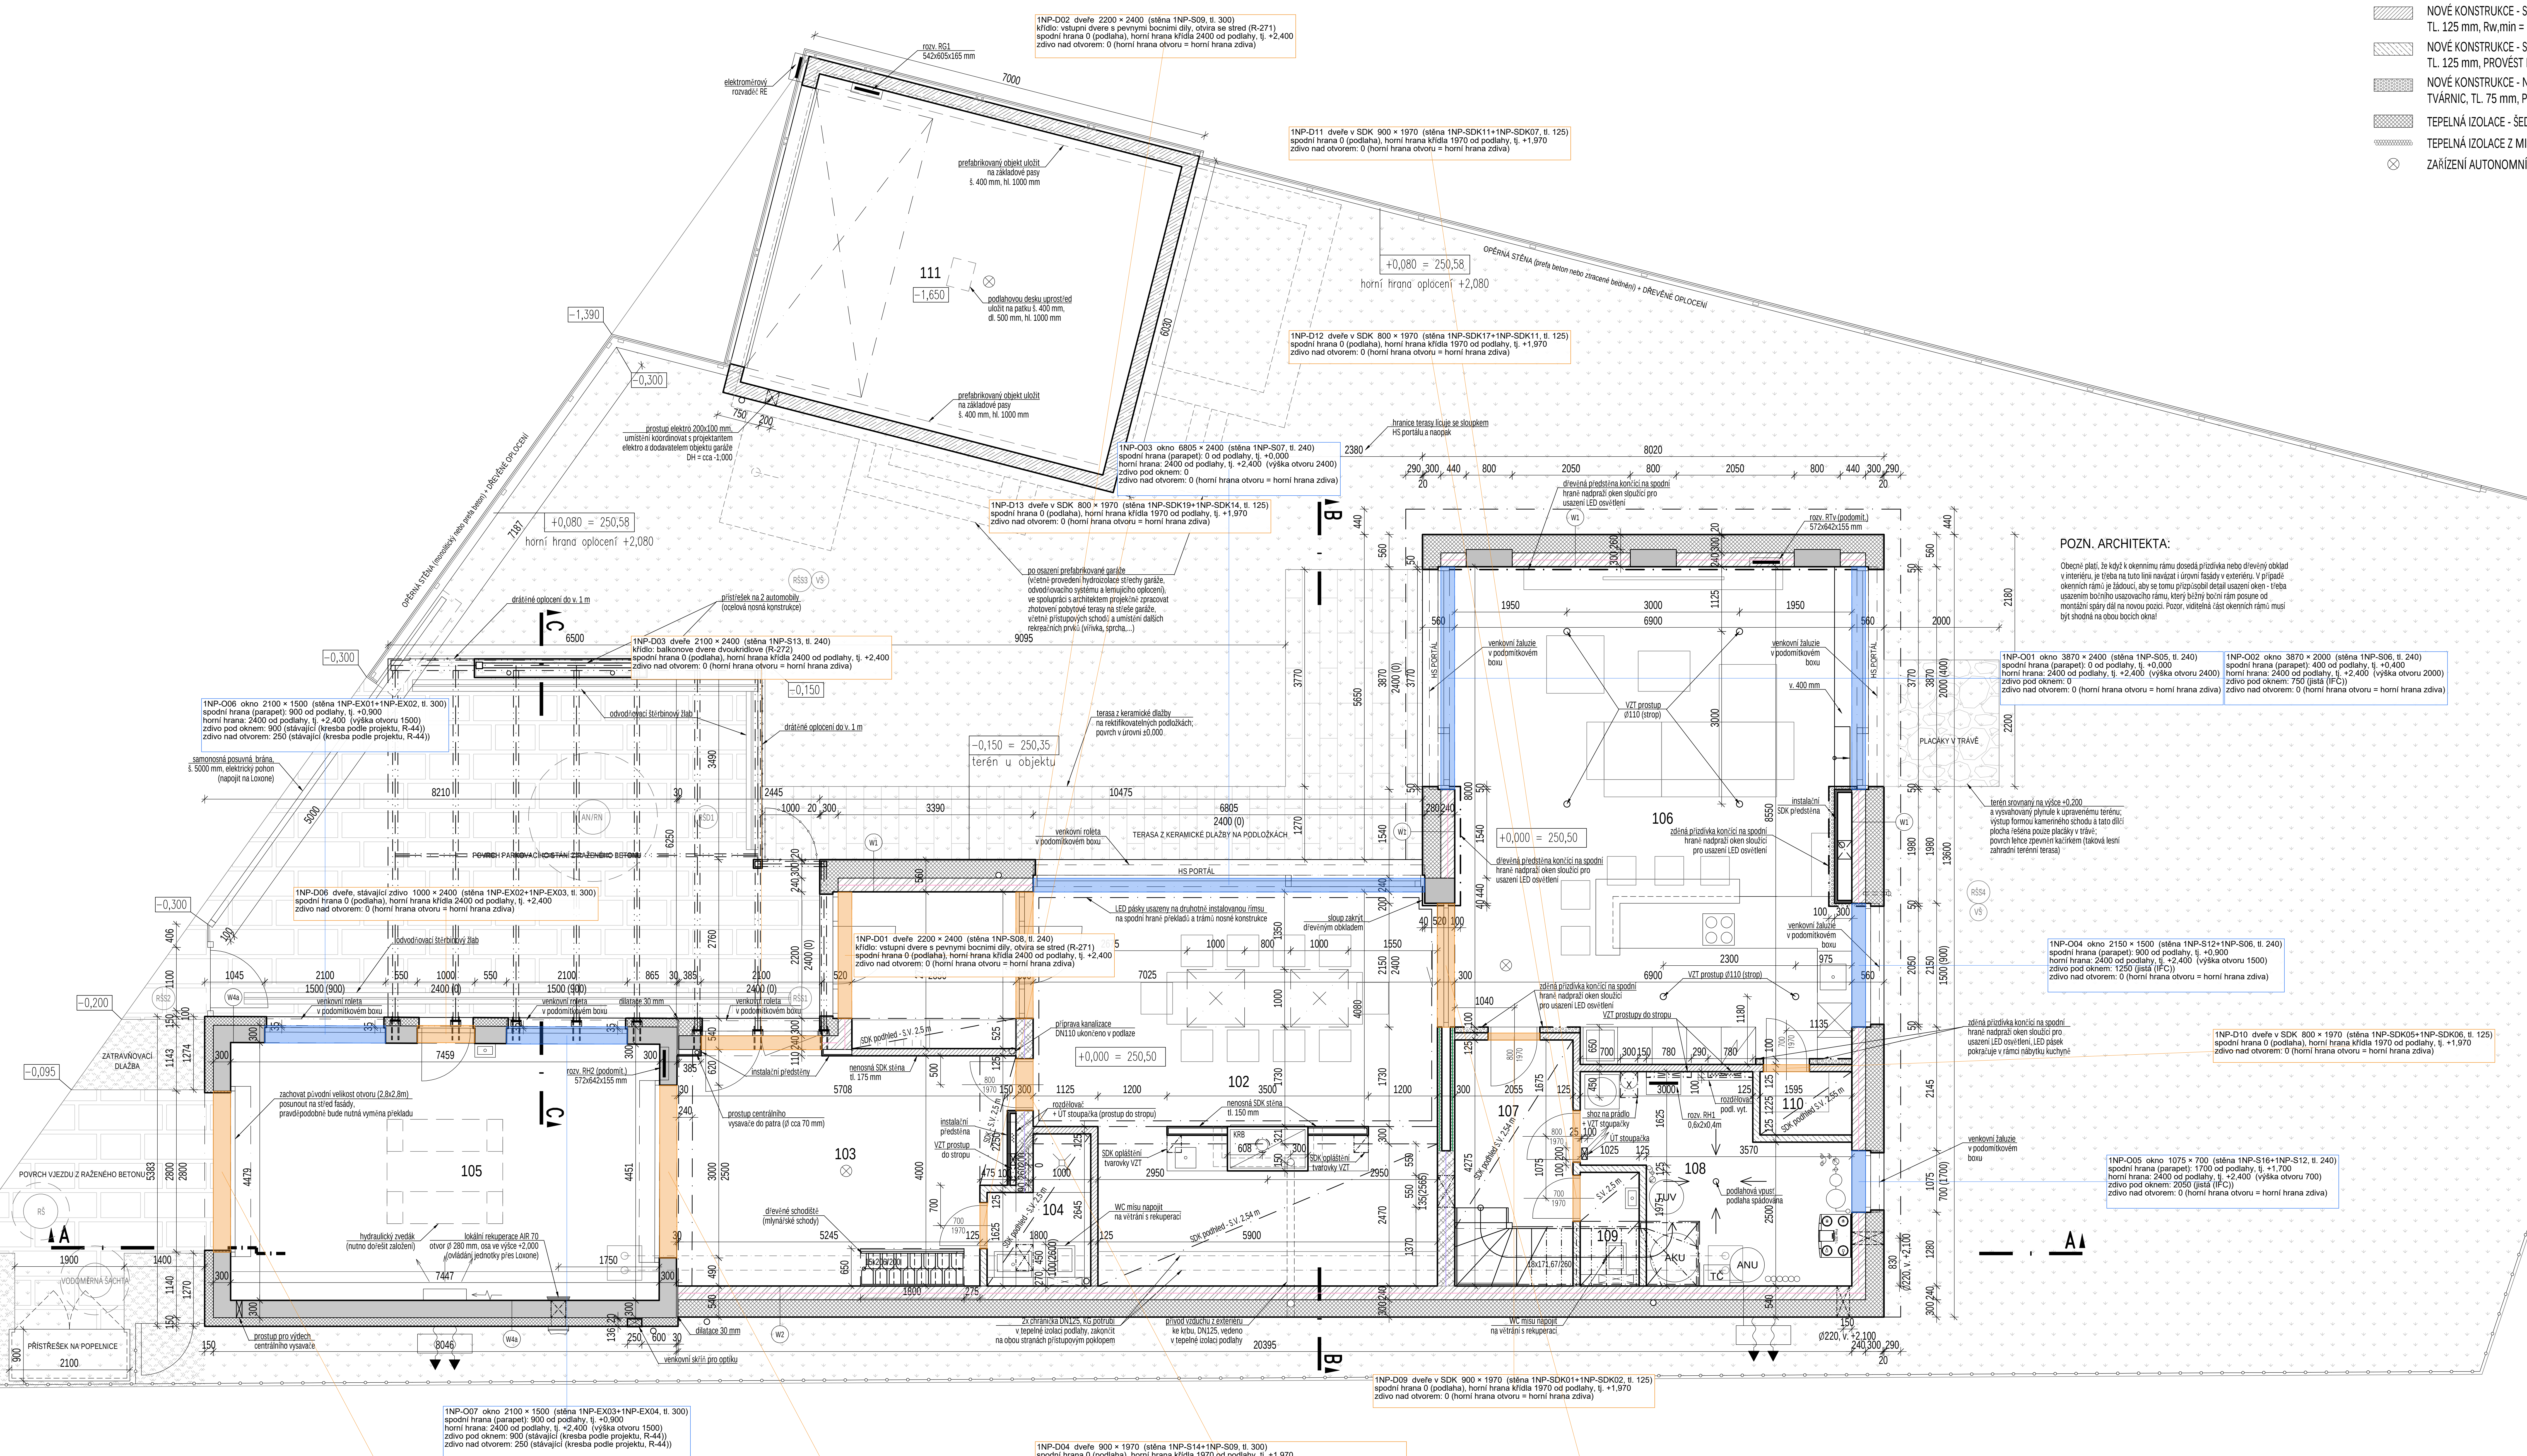

111
−1,650
podlahovou desku uprostřed uložit na patku š. 400 mm, dl. 500 mm, hl. 1000 mm
prefabrikovaný objekt uložit na základové pasy š. 400 mm, hl. 1000 mm
7000
6030
rozv. RG1 542x605x165 mm
elektroměrový rozvaděč RE
+0,080 = 250,58
horní hrana oplocení +2,080
OPĚRNÁ STĚNA (prefa beton nebo ztracené bednění) + DŘEVĚNÉ OPLOCENÍ
DŘEVĚNÉ OPLOCENÍ + POGRABOVÉ DESKY
hranice terasy lícuje se sloupkem HS portálu a naopak
po osazení prefabrikované garáže (včetně provedení hydroizolace střechy garáže, odvodňovacího systému a lemujícího oplocení), ve spolupráci s architektem projekčně zpracovat zhotovení pobytové terasy na střeše garáže,
prostup elektro 200x100 mm umístění koordinovat s projektantem elektro a dodavatelem objektu garáže
−1,390
−0,300
−0,150
−0,200
−0,095
+0,190
−0,150 = 250,35
terén u objektu
drátěné oplocení do v. 1 m
přístřešek na 2 automobily (ocelová nosná konstrukce)
odvodňovací štěrbinový žlab
samonosná posuvná brána, š. 5000 mm, elektrický pohon (napojit na Loxone)
POVRCH PARKOVACÍHO STÁNÍ Z RAŽENÉHO BETONU
POVRCH VJEZDU Z RAŽENÉHO BETONU
ZATRAVŇOVACÍ DLAŽBA
VODOMĚRNÁ ŠACHTA
PŘÍSTŘEŠEK NA POPELNICE
terasa z keramické dlažby na rektifikovatelných podložkách; povrch v úrovni ±0,000
TERASA Z KERAMICKÉ DLAŽBY NA PODLOŽKÁCH
HS PORTÁL
LED pásky usazeny na druhotně instalovanou římsu na spodní hraně překladů a trámů nosné konstrukce
dřevěná předstěna končící na spodní hraně nadpraží oken sloužící pro usazení LED osvětlení
zděná přizdívka končící na spodní hraně nadpraží oken sloužící pro usazení LED osvětlení, LED pásek pokračuje v rámci nábytku kuchyně
venkovní žaluzie v podomítkovém boxu
venkovní roleta v podomítkovém boxu
PLACÁKY V TRÁVĚ
terén srovnaný na výšce +0,200 a vysvahovaný plynule k upravenému terénu; výstup formou kamenného schodu a tato dílčí plocha řešena pouze placáky v trávě; povrch lehce zpevněn kačírkem (taková lesní zahradní terénní terasa)
+0,000 = 250,50
příprava kanalizace DN110 ukončeno v podlaze
SDK podhled - S.V. 2,5 m
105
102
103
104
106
107
108
109
110
RŠS1
RŠS2
RŠS3
RŠS4
RŠD1
VŠ
AN/RN
W1
W2
W4a
TČ
AKU
ANU
prostup pro výdech centrálního vysavače
dilatace 30 mm
venkovní skříň pro optiku
2x chránička DN125, KG potrubí v tepelné izolaci podlahy, zakončit na obou stranách přístupovým poklopem
přívod vzduchu z exteriéru ke krbu, DN125, vedeno v tepelné izolaci podlahy
WC mísu napojit na větrání s rekuperací
8046
20395
8020
10475
6805
8210
6500
5000
13600
A
B
C

1NP-D02 dveře 2200 × 2400 (stěna 1NP-S09, tl. 300)
křídlo: vstupni dvere s pevnymi bocnimi dily, otvira se stred (R-271)
spodní hrana 0 (podlaha), horní hrana křídla 2400 od podlahy, tj. +2,400
zdivo nad otvorem: 0 (horní hrana otvoru = horní hrana zdiva)

1NP-D11 dveře v SDK 900 × 1970 (stěna 1NP-SDK11+1NP-SDK07, tl. 125)
spodní hrana 0 (podlaha), horní hrana křídla 1970 od podlahy, tj. +1,970
zdivo nad otvorem: 0 (horní hrana otvoru = horní hrana zdiva)

1NP-D12 dveře v SDK 800 × 1970 (stěna 1NP-SDK17+1NP-SDK11, tl. 125)
spodní hrana 0 (podlaha), horní hrana křídla 1970 od podlahy, tj. +1,970
zdivo nad otvorem: 0 (horní hrana otvoru = horní hrana zdiva)

1NP-O03 okno 6805 × 2400 (stěna 1NP-S07, tl. 240)
spodní hrana (parapet): 0 od podlahy, tj. +0,000
horní hrana: 2400 od podlahy, tj. +2,400 (výška otvoru 2400)
zdivo pod oknem: 0
zdivo nad otvorem: 0 (horní hrana otvoru = horní hrana zdiva)

1NP-D13 dveře v SDK 800 × 1970 (stěna 1NP-SDK19+1NP-SDK14, tl. 125)
spodní hrana 0 (podlaha), horní hrana křídla 1970 od podlahy, tj. +1,970
zdivo nad otvorem: 0 (horní hrana otvoru = horní hrana zdiva)

1NP-D03 dveře 2100 × 2400 (stěna 1NP-S13, tl. 240)
křídlo: balkonove dvere dvoukridlove (R-272)
spodní hrana 0 (podlaha), horní hrana křídla 2400 od podlahy, tj. +2,400
zdivo nad otvorem: 0 (horní hrana otvoru = horní hrana zdiva)

1NP-O06 okno 2100 × 1500 (stěna 1NP-EX01+1NP-EX02, tl. 300)
spodní hrana (parapet): 900 od podlahy, tj. +0,900
horní hrana: 2400 od podlahy, tj. +2,400 (výška otvoru 1500)
zdivo pod oknem: 900 (stávající (kresba podle projektu, R-44))
zdivo nad otvorem: 250 (stávající (kresba podle projektu, R-44))

1NP-D06 dveře, stávající zdivo 1000 × 2400 (stěna 1NP-EX02+1NP-EX03, tl. 300)
spodní hrana 0 (podlaha), horní hrana křídla 2400 od podlahy, tj. +2,400
zdivo nad otvorem: 0 (horní hrana otvoru = horní hrana zdiva)

1NP-D01 dveře 2200 × 2400 (stěna 1NP-S08, tl. 240)
křídlo: vstupni dvere s pevnymi bocnimi dily, otvira se stred (R-271)
spodní hrana 0 (podlaha), horní hrana křídla 2400 od podlahy, tj. +2,400
zdivo nad otvorem: 0 (horní hrana otvoru = horní hrana zdiva)

1NP-O01 okno 3870 × 2400 (stěna 1NP-S05, tl. 240)
spodní hrana (parapet): 0 od podlahy, tj. +0,000
horní hrana: 2400 od podlahy, tj. +2,400 (výška otvoru 2400)
zdivo pod oknem: 0
zdivo nad otvorem: 0 (horní hrana otvoru = horní hrana zdiva)

1NP-O02 okno 3870 × 2000 (stěna 1NP-S06, tl. 240)
spodní hrana (parapet): 400 od podlahy, tj. +0,400
horní hrana: 2400 od podlahy, tj. +2,400 (výška otvoru 2000)
zdivo pod oknem: 750 (jistá (IFC))
zdivo nad otvorem: 0 (horní hrana otvoru = horní hrana zdiva)

1NP-O04 okno 2150 × 1500 (stěna 1NP-S12+1NP-S06, tl. 240)
spodní hrana (parapet): 900 od podlahy, tj. +0,900
horní hrana: 2400 od podlahy, tj. +2,400 (výška otvoru 1500)
zdivo pod oknem: 1250 (jistá (IFC))
zdivo nad otvorem: 0 (horní hrana otvoru = horní hrana zdiva)

1NP-D10 dveře v SDK 800 × 1970 (stěna 1NP-SDK05+1NP-SDK06, tl. 125)
spodní hrana 0 (podlaha), horní hrana křídla 1970 od podlahy, tj. +1,970
zdivo nad otvorem: 0 (horní hrana otvoru = horní hrana zdiva)

1NP-O05 okno 1075 × 700 (stěna 1NP-S16+1NP-S12, tl. 240)
spodní hrana (parapet): 1700 od podlahy, tj. +1,700
horní hrana: 2400 od podlahy, tj. +2,400 (výška otvoru 700)
zdivo pod oknem: 2050 (jistá (IFC))
zdivo nad otvorem: 0 (horní hrana otvoru = horní hrana zdiva)

1NP-D09 dveře v SDK 900 × 1970 (stěna 1NP-SDK01+1NP-SDK02, tl. 125)
spodní hrana 0 (podlaha), horní hrana křídla 1970 od podlahy, tj. +1,970
zdivo nad otvorem: 0 (horní hrana otvoru = horní hrana zdiva)

1NP-O07 okno 2100 × 1500 (stěna 1NP-EX03+1NP-EX04, tl. 300)
spodní hrana (parapet): 900 od podlahy, tj. +0,900
horní hrana: 2400 od podlahy, tj. +2,400 (výška otvoru 1500)
zdivo pod oknem: 900 (stávající (kresba podle projektu, R-44))
zdivo nad otvorem: 250 (stávající (kresba podle projektu, R-44))

1NP-D07 dveře, stávající zdivo 2800 × 2800 (stěna 1NP-EX07+1NP-EX06, tl. 300)
spodní hrana 0 (podlaha), horní hrana křídla 2800 od podlahy, tj. +2,800
zdivo nad otvorem: 0 (horní hrana otvoru = horní hrana zdiva)

1NP-D08 dveře, stávající zdivo 3000 × 2500 (stěna 1NP-EX08+1NP-EX05, tl. 300)
spodní hrana 0 (podlaha), horní hrana křídla 2500 od podlahy, tj. +2,500
zdivo nad otvorem: 0 (horní hrana otvoru = horní hrana zdiva)

1NP-D04 dveře 900 × 1970 (stěna 1NP-S14+1NP-S09, tl. 300)
spodní hrana 0 (podlaha), horní hrana křídla 1970 od podlahy, tj. +1,970
zdivo nad otvorem: neurčeno (max 430 mm do DH věnce), varianta překladu = otázka staviteli 2 (E132)

1NP-D05 dveře 2150 × 2400 (stěna 1NP-S15+1NP-S05, tl. 300)
spodní hrana 0 (podlaha), horní hrana křídla 2400 od podlahy, tj. +2,400
zdivo nad otvorem: 0 (horní hrana otvoru = horní hrana zdiva)

POZN. ARCHITEKTA:

Obecně platí, že když k okennímu rámu dosedá přizdívka nebo dřevěný obklad v interiéru, je třeba na tuto linii navázat i úrovní fasády v exteriéru. V případě okenních rámů je žádoucí, aby se tomu přizpůsobil detail usazení oken - třeba usazením bočního usazovacího rámu, který běžný boční rám posune od montážní spáry dál na novou pozici. Pozor, viditelná část okenních rámů musí být shodná na obou bocích okna!

LEGENDA KONSTRUKCÍ - PŮDORYS

- ▒ STÁVAJÍCÍ KONSTRUKCE - SMÍŠENÉ ZDIVO (včetně omítky)
- ▒ NOVÉ KONSTRUKCE - ŽELEZOBETONOVÉ
- ▨ NOVÉ KONSTRUKCE - NOSNÉ ZDIVO Z VÁPENOPÍSKOVÝCH BLOKŮ VAPIS TL. 300 mm, PROVÉST DLE TECHNOLOG. PŘEDPISU
- ▨ NOVÉ KONSTRUKCE - NOSNÉ ZDIVO Z VÁPENOPÍSKOVÝCH BLOKŮ VAPIS TL. 240 mm, PROVÉST DLE TECHNOLOG. PŘEDPISU
- ▨ NOVÉ KONSTRUKCE - NOSNÉ ZDIVO Z VÁPENOPÍSKOVÝCH BLOKŮ VAPIS TL. 200 mm, PROVÉST DLE TECHNOLOG. PŘEDPISU
- ▨ NOVÉ KONSTRUKCE - SÁDROKARTONOVÉ PŘÍČKY DVOJITĚ OPLÁŠTĚNÉ TL. 125 mm, Rw,min = 57 dB, PROVÉST DLE TECHNOLOG. PŘEDPISU
- ▨ NOVÉ KONSTRUKCE - SÁDROKARTONOVÉ PŘÍČKY JEDNODUŠE OPLÁŠTĚNÉ TL. 125 mm, PROVÉST DLE TECHNOLOG. PŘEDPISU
- ▒ NOVÉ KONSTRUKCE - NENOSNÉ PŘÍČKY A PŘIZDÍVKY Z VÁPENOPÍSKOVÝCH TVÁRNIC, TL. 75 mm, PROVÉST DLE TECHNOLOG.PŘEDPISU
- ▩ TEPELNÁ IZOLACE - ŠEDÝ POLYSTYREN
- ∿ TEPELNÁ IZOLACE Z MINERÁLNÍCH VLÁKEN
- ⊗ ZAŘÍZENÍ AUTONOMNÍ DETEKCE A SIGNALIZACE KOUŘE

TABULKA MÍSTNOSTÍ

č.m.	místnost	plocha (m2)	s.v. (m)	podlaha	stěny	strop
101	Vstupní prostor	7,8	2,70 a 2,5	dlažba	malba	beton, SDK + malba
102	Hala - jídelna	43,6	2,70 a 2,54	dlažba	malba/obkl.	beton, SDK + malba
103	Dílna	22,5	2,70	stěrka	malba	beton
104	Sprcha, WC	3,9	2,50	dlažba	malba/obkl.	SDK + malba
105	Garáž	33,3	5,97	stěrka	malba	beton
106	Obývací pokoj, kuchyně	57,3	2,70 a 2,60	dlažba	malba/obkl.	beton
107	Hala - schodiště	8,8	2,54	dlažba	malba	SDK + malba
108	Technická místnost	13,1	2,70	dlažba	malba	beton
109	WC	2,0	1,50 - 2,50	dlažba	malba/obkl.	SDK + malba
110	Spíž	1,8	2,55	dlažba	malba/obkl.	SDK + malba
	Celkem	192,6				
111	Samostatná samonosná dvojgaráž	36,0	prefabrikovaná betonová kce 7x6,03x2,47m; dodáno vcelku			

Revize:	Obsah změny:	Autor:	Datum:
00	-	-	-

Název akce:
NOVOSTAVBA RODINNÉHO DOMU

Místo stavby: adresa stavby neuvedena
Objednatel: investor
Paré:
Generální projektant:
Profese:
Projektant: projektantka
Projekční tým: projektantka
Kontroloval:
Autorizační razítko:
Formát: -
Měřítko: 1:50
Část: ARCHITEKTONICKO - STAVEBNÍ
Číslo projektu:
Datum: 09/2026
Stupeň: -
Vydal: projektantka
Obsah výkresu:

PŮDORYS 1.NP

Číslo výkresu: D11-01

DOKUMENTACE JE DUSEVNIM MAJETKEM FIRMY RECOC S.R.O. A NESMI BYT POUZITA BEZ JEJIHO VEDOMI