PŘEKLADY - co je nad každým otvorem v nosném zdivu (odvozeno z Nzu A-A, typ určí krok ST): (1NP, překlady-1NP.pdf)
otvor okna: spodní z horní hrana
dveře v nosném zdivu (v SDK ale nakreslí, překlad tam není)
mezera ve zdivu bez výplně / bez kóty

1NP-D02 překlad nad dveřmi 2200 mm, zdivo tl. 300
horní hrana křídla 2400; zdivo nad otvorem: 0 (horní hrana otvoru = horní hrana zdiva)
překlad NEURČEN ve výkrese: varianta (hotový překlad + zdivo / ŽB překlad + zdivo / ŽB ke stropu) podle odpovědi stavitele na otázku 2 (E132, R-276, R-281); v SDK příčkách překlady nejsou

1NP-D05 překlad nad dveřmi 2150 mm, zdivo tl. 300
horní hrana křídla 2400; zdivo nad otvorem: 0 (horní hrana otvoru = horní hrana zdiva)
překlad NEURČEN ve výkrese: varianta (hotový překlad + zdivo / ŽB překlad + zdivo / ŽB ke stropu) podle odpovědi stavitele na otázku 2 (E132, R-276, R-281); v SDK příčkách překlady nejsou

1NP-O01 překlad nad oknem 3870 mm, zdivo tl. 240
horní hrana okna +2,400 + spodní hrana ZB věnce 300 mm (+2,400 až +2,700), věnec slouží jako překlad
zdroj: řez A-A v DWG, TZ statiky (věnec 300, mistý 200) [odvození: platí pro stěny, které řez kryje]

1NP-O04 překlad nad oknem 2150 mm, zdivo tl. 240
horní hrana okna +2,400 + spodní hrana ZB věnce 300 mm (+2,400 až +2,700), věnec slouží jako překlad
zdroj: řez A-A v DWG, TZ statiky (věnec 300, mistý 200) [odvození: platí pro stěny, které řez kryje]

1NP-O02 překlad nad oknem 3870 mm, zdivo tl. 240
horní hrana okna +2,400 + spodní hrana ZB věnce 300 mm (+2,400 až +2,700), věnec slouží jako překlad
zdroj: řez A-A v DWG, TZ statiky (věnec 300, mistý 200) [odvození: platí pro stěny, které řez kryje]

1NP-O03 překlad nad oknem 6805 mm, zdivo tl. 240
horní hrana okna +2,400 + spodní hrana ZB věnce 300 mm (+2,400 až +2,700), věnec slouží jako překlad
zdroj: řez A-A v DWG, TZ statiky (věnec 300, mistý 200) [odvození: platí pro stěny, které řez kryje]

1NP-O05 překlad nad oknem 1075 mm, zdivo tl. 240
horní hrana okna +2,400 + spodní hrana ZB věnce 300 mm (+2,400 až +2,700), věnec slouží jako překlad
zdroj: řez A-A v DWG, TZ statiky (věnec 300, mistý 200) [odvození: platí pro stěny, které řez kryje]

1NP-D03 překlad nad dveřmi 2100 mm, zdivo tl. 240
horní hrana křídla 2400; zdivo nad otvorem: 0 (horní hrana otvoru = horní hrana zdiva)
překlad NEURČEN ve výkrese: varianta (hotový překlad + zdivo / ŽB překlad + zdivo / ŽB ke stropu) podle odpovědi stavitele na otázku 2 (E132, R-276, R-281); v SDK příčkách překlady nejsou

1NP-D04 překlad nad dveřmi 900 mm, zdivo tl. 300
horní hrana křídla 1970; zdivo nad otvorem: neurčeno (max 430 mm do DH věnce), varianta překladu = otázka stavitel 2 (E132)
překlad NEURČEN ve výkrese: varianta (hotový překlad + zdivo / ŽB překlad + zdivo / ŽB ke stropu) podle odpovědi stavitele na otázku 2 (E132, R-276, R-281); v SDK příčkách překlady nejsou

1NP-D01 překlad nad dveřmi 2200 mm, zdivo tl. 240
horní hrana křídla 2400; zdivo nad otvorem: 0 (horní hrana otvoru = horní hrana zdiva)
překlad NEURČEN ve výkrese: varianta (hotový překlad + zdivo / ŽB překlad + zdivo / ŽB ke stropu) podle odpovědi stavitele na otázku 2 (E132, R-276, R-281); v SDK příčkách překlady nejsou

LEGENDA KONSTRUKCÍ - PŮDORYS

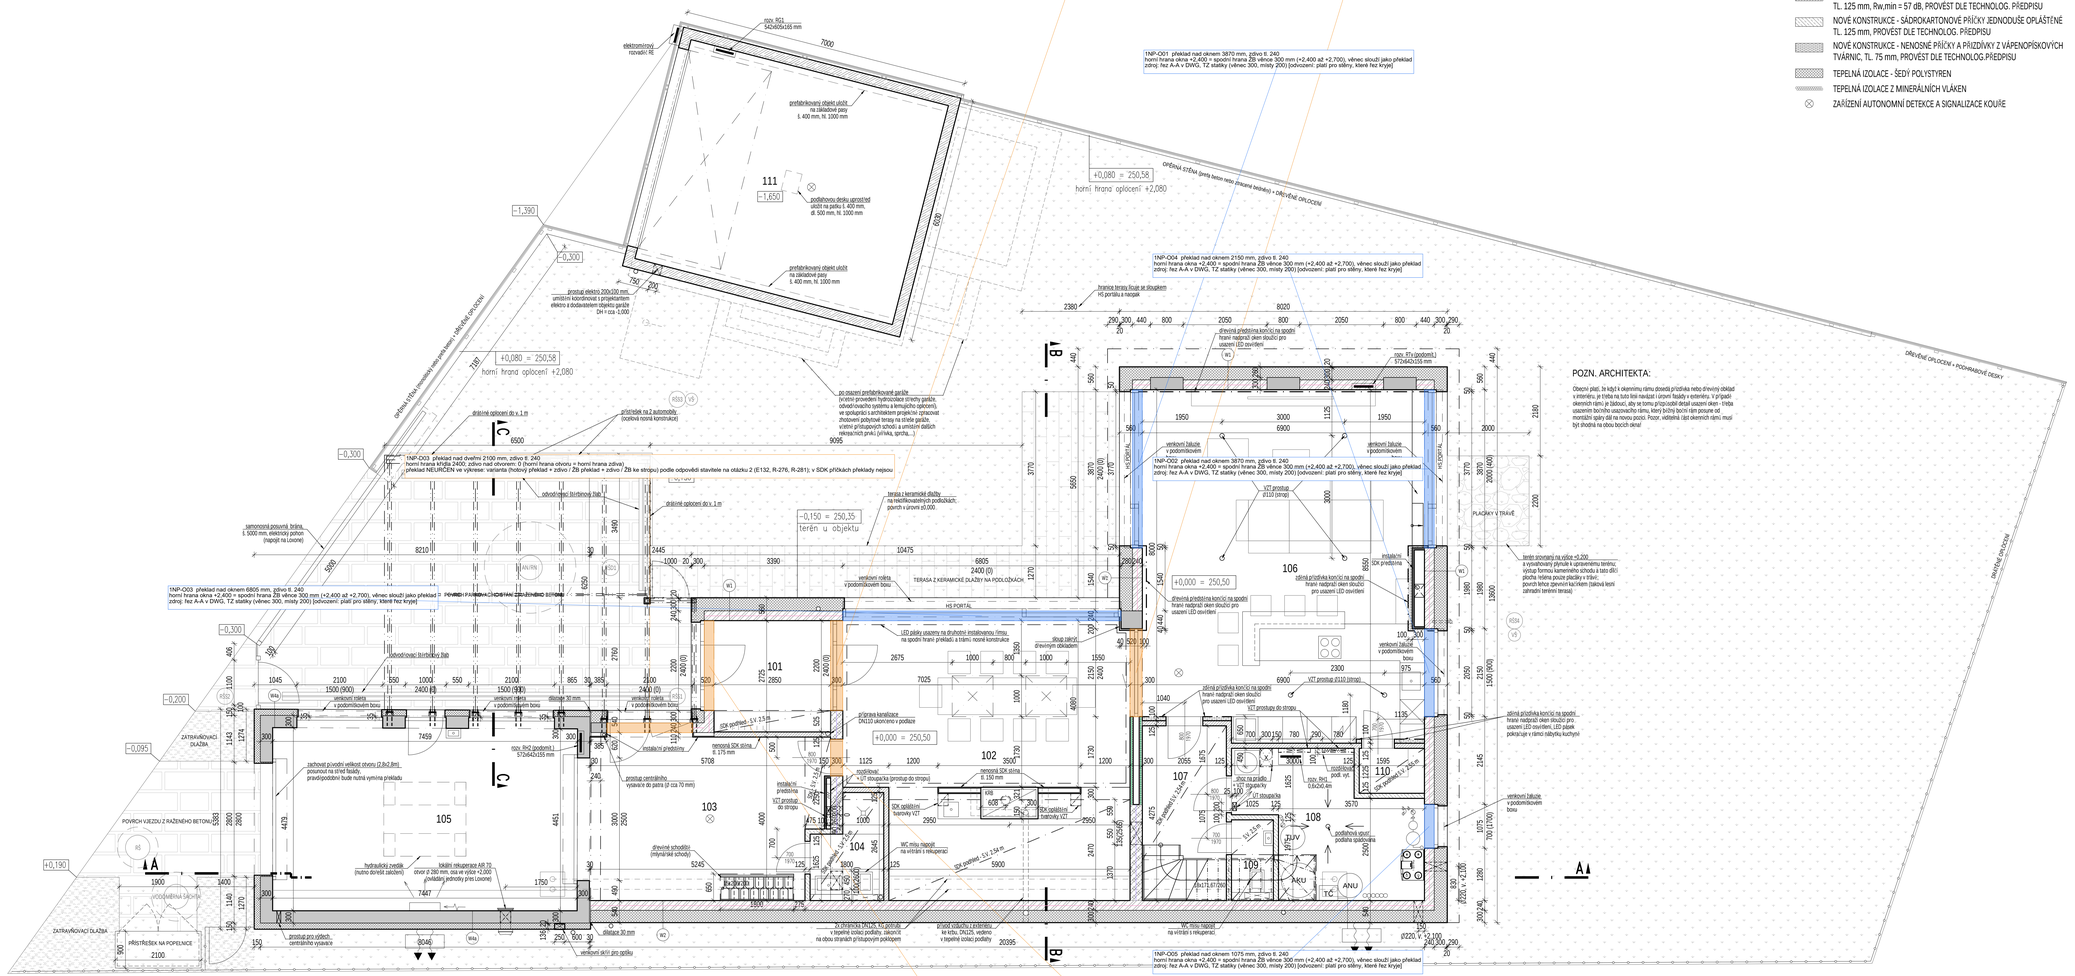
- STÁVAJÍCÍ KONSTRUKCE - SMÍŠENÉ ZDIVO (včetně omítky)
- NOVÉ KONSTRUKCE - ŽELEZOBETONOVÉ
- NOVÉ KONSTRUKCE - NOSNÉ ZDIVO Z VÁPENOPÍSKOVÝCH BLOKŮ VAPIS TL. 300 mm, PROVĚST DLE TECHNOLOG. PŘEDPISU
- NOVÉ KONSTRUKCE - NOSNÉ ZDIVO Z VÁPENOPÍSKOVÝCH BLOKŮ VAPIS TL. 240 mm, PROVĚST DLE TECHNOLOG. PŘEDPISU
- NOVÉ KONSTRUKCE - NOSNÉ ZDIVO Z VÁPENOPÍSKOVÝCH BLOKŮ VAPIS TL. 200 mm, PROVĚST DLE TECHNOLOG. PŘEDPISU
- NOVÉ KONSTRUKCE - SÁDROKARTONOVÉ PŘÍČKY DVOJITĚ OPLÁŠTĚNÉ TL. 125 mm, Rw,min = 57 dB, PROVĚST DLE TECHNOLOG. PŘEDPISU
- NOVÉ KONSTRUKCE - SÁDROKARTONOVÉ PŘÍČKY JEDNODUŠE OPLÁŠTĚNÉ TL. 125 mm, PROVĚST DLE TECHNOLOG. PŘEDPISU
- NOVÉ KONSTRUKCE - NENOSNÉ PŘÍČKY A PŘIZDÍVKY Z VÁPENOPÍSKOVÝCH TVÁRNIC, TL. 75 mm, PROVĚST DLE TECHNOLOG.PŘEDPISU
- TEPELNÁ IZOLACE - ŠEDÝ POLYSTYREN
- TEPELNÁ IZOLACE Z MINERÁLNÍCH VLÁKEN
- ZAŘÍZENÍ AUTONOMNÍ DETEKCE A SIGNALIZACE KOUŘE

TABULKA MÍSTNOSTÍ

č.m.	místnost	plocha (m2)	s.v. (m)	podlaha	stěny	strop
101	Vstupní prostor	7,8	2,70 a 2,5	dlažba	malba	beton, SDK + malba
102	Hala - jídelna	43,6	2,70 a 2,54	dlažba	malba/obkl.	beton, SDK + malba
103	Dílna	22,5	2,70	stěrka	malba	beton
104	Sprcha, WC	3,9	2,50	dlažba	malba/obkl.	SDK + malba
105	Garáž	33,3	5,97	stěrka	malba	beton
106	Obývací pokoj, kuchyně	57,3	2,70 a 2,60	dlažba	malba/obkl.	beton
107	Hala - schodiště	8,8	2,54	dlažba	malba	SDK + malba
108	Technická místnost	13,1	2,70	dlažba	malba	beton
109	WC	2,0	1,50 - 2,50	dlažba	malba/obkl.	SDK + malba
110	Spíž	1,8	2,55	dlažba	malba/obkl.	SDK + malba
	Celkem	192,6				
111	Samostatná samonosná dvojgaráž	36,0	prefabrikovaná betonová kce 7x6,03x2,47m; dodáno vcelku			

POZN. ARCHITEKTA:

Obecně platí, že kdyţ k okennímu rámu dosedá příčka nebo dřevěný obklad v interiéru, je třeba na tuto linii nadsázet i izolaci fasády v exteriéru. V případě okenních rámů je žádoucí, aby se tomu přizpůsobil detail usazení oken - třeba usazením bochníku usazovacího rámu, který boční lící rámu posune od montážní spáry dál na novou pozici. Pozor, viditelná část okenních rámů musí být shodná na obou bocích okna!


+0,080 = 250,58
horní hrana oplocení +2,080
−0,150 = 250,35
terén u objektu
+0,000 = 250,50
−0,300
−0,200
−0,095
+0,190
−1,390
−1,650
prefabrikovaný objekt uložit na základové pasy tl. 400 mm, hl. 1000 mm
podlahovou desku upronstřed uložit na patku tl. 400 mm, dl. 500 mm, hl. 1000 mm
prostup elektro 200x100 mm, umístění koordinovat s projektantem elektro a dodavatelem objektu garáže DH = cca 1,000
po osazení prefabrikované garáže (vnitřní provedení hydroizolace stěny garáže, odvodňovací systémy a ikmujícího oplocení), ve spolupráci s architektem projektuje oprávněný zhotovitel jednotlivé stavby na střeše garáže, včetně přístupových schodů a umístění dalších prvků/technických prvků (příhrada, sprcha, ...)
přístřešek na 2 automobily (ocelová nosná konstrukce)
dřevěné oplocení dl/v x 1 m
samonosná posuvná brána, L 5000 mm, elektrický pohon (napojit na Losonie)
odvodňovací štěrbinový žlab
terasa z keramické dlažby na nekřišťálovém podložkách, sklonu k úrovni zt.0.000
TERASA Z KERAMICKÉ DLAŽBY NA PODLOŽKÁCH
HS PORTÁL
LED pásky usazeny na druhotné instalovanou rímsu na spodní hraně překladu a trámů nosné konstrukce
sloup nátěr dřevěných obkladem
dřevěná předsázka konců na spodní hraně nadpraží oken slouží pro usazení LED osvětlení
venkovní roleta v podomítkovém boxu
venkovní žaluzie v podomítkovém boxu
VZT prostup Ø110 (strop)
VZT prostup Ø160 (strop)
VZT prostup Ø200 (strop)
VZT prostupy do stropu
instalační předstěna
SDK opláštění hořlavého VZT
nenosná SDK stěna tl. 175 mm
nenosná SDK stěna tl. 150 mm
podlahová vpusť, podlaha spádovaná
WC mísa napojit na větrání s rekuperací
WC bidet napojit na větrání s rekuperací
dřevěné schodiště (mýtnické schody)
hydraulický zvedák (nutno dovézt sebou)
klidním rekuperace AIR 70 (ovládání jednotky přes Losonie)
prostupy pro výdech centrálního vysavače
ZATRAVŇOVACÍ DLAŽBA
POVRCH VJEZDU Z RAŽENÉHO BETONU
PŘÍSTŘEŠEK NA POPELNICE
VODOMĚRNÁ ŠACHTA
ŠIKMÁ STŘECHA
ŠIKMÁ STŘECHA - ROVNOBĚŽNÁ S HORNÍ HRANOU ZDIVA
DŘEVĚNÉ OPLOCENÍ + PODHLEDOVÉ DESKY
DŘEVĚNÉ OPLOCENÍ
PLACHTY V TRÁVĚ
terén srovnaný na výšce +0,200 a vyrušovaný plynule k upravenému terénu, výstup formou kamenného schodu a tato dílčí plocha hrána pouze plachty v trávě, povrch krhce zpevnění kačírkem (takovú lezní zátrabní terénní terasa)
venkovní žaluzie v podomítkovém boxu
venkovní žaluzie v podomítkovém boxu
venkovní skříň pro popelnu
kanalizační přípojka
vodovodní přípojka
plynovodní přípojka
elektro/silnoproud rozvaděč RE
prefabrikovaný objekt uložit na základové pasy tl. 400 mm, hl. 1000 mm
hranice terasy řešit se sloupkem HS portálu a nacpák
dřevěná předsázka konců na spodní hraně nadpraží oken slouží pro usazení LED osvětlení
nízký RTv (podomítk.) 572x642x155 mm
nízký RTv (podomítk.) 572x642x155 mm
nízký RK2 (podomítk.) 572x642x155 mm
nízký RK2 (podomítk.) 572x642x155 mm
nízký RK1 (podomítk.) 572x642x155 mm
nízký RK1 (podomítk.) 572x642x155 mm
nízký RK2 (podomítk.) 572x642x155 mm
nízký RK2 (podomítk.) 572x642x155 mm
nízký RK2