OTVORY: šířka, spodní hrana (parapet), horní hrana; výšky od podlahy podlaží a absolutně (2NP, otvory-2NP.pdf)

- 🟦 otvor okna: spodní a horní hrana
- 🟧 dveře v nosném zdivu (v SDK se nekreslí, překlad tam není)
- ⬜ mezera ve zdivu bez výplně / bez kóty
- 🟥 ŽB parapet podle TZ statiky (není zdivo)

LEGENDA KONSTRUKCÍ - PŮDORYS

▬	STÁVAJÍCÍ KONSTRUKCE - SMÍŠENÉ ZDIVO (včetně omítky)
▬	NOVÉ KONSTRUKCE - ŽELEZOBETONOVÉ
▩	NOVÉ KONSTRUKCE - NOSNÉ ZDIVO Z VÁPENOPÍSKOVÝCH BLOKŮ VAPIS TL. 300 mm, PROVÉST DLE TECHNOLOG. PŘEDPISU
▨	NOVÉ KONSTRUKCE - NOSNÉ ZDIVO Z VÁPENOPÍSKOVÝCH BLOKŮ VAPIS TL. 240 mm, PROVÉST DLE TECHNOLOG. PŘEDPISU
▩	NOVÉ KONSTRUKCE - NOSNÉ ZDIVO Z VÁPENOPÍSKOVÝCH BLOKŮ VAPIS TL. 200 mm, PROVÉST DLE TECHNOLOG. PŘEDPISU
▨	NOVÉ KONSTRUKCE - SÁDROKARTONOVÉ PŘÍČKY DVOJITĚ OPLÁŠTĚNÉ TL. 125 mm, Rw,min = 57 dB, PROVÉST DLE TECHNOLOG. PŘEDPISU
▧	NOVÉ KONSTRUKCE - SÁDROKARTONOVÉ PŘÍČKY JEDNODUŠE OPLÁŠTĚNÉ TL. 125 mm, PROVÉST DLE TECHNOLOG. PŘEDPISU
▒	NOVÉ KONSTRUKCE - NENOSNÉ PŘÍČKY A PŘIZDÍVKY Z VÁPENOPÍSKOVÝCH TVÁRNIC, TL. 75 mm, PROVÉST DLE TECHNOLOG.PŘEDPISU
▦	TEPELNÁ IZOLACE - ŠEDÝ POLYSTYREN
〰	TEPELNÁ IZOLACE Z MINERÁLNÍCH VLÁKEN
⊗	ZAŘÍZENÍ AUTONOMNÍ DETEKCE A SIGNALIZACE KOUŘE

TABULKA MÍSTNOSTÍ

č.m.	místnost	plocha (m2)	s.v. (m)	podlaha	stěny	strop
201	Hala	17,5	2,60	dlažba	malba	SDK + malba
202	Koupelna, WC	5,2	2,60	dlažba	malba/obkl.	SDK + malba
203	Šatna	11,1	2,60	dlažba	malba	SDK + malba
204	Koupelna, WC	5,5	2,60	dlažba	malba/obkl.	SDK + malba
205	Ložnice	14,1	2,70	dlažba	malba	SDK + malba
206	Ložnice	13,7	2,70	dlažba	malba	SDK + malba
207	Ložnice	15,6	2,70	dlažba	malba	SDK + malba
208	Pracovna	24,1	2,70	dlažba	malba	SDK + malba
209	Sklad, pracovna	23,2	2,70	dlažba	malba	SDK + malba
	Celkem	115,0				
210	Pobytová část střechy - terasa	22,7				
211	Nepochozí část střechy	26,0				

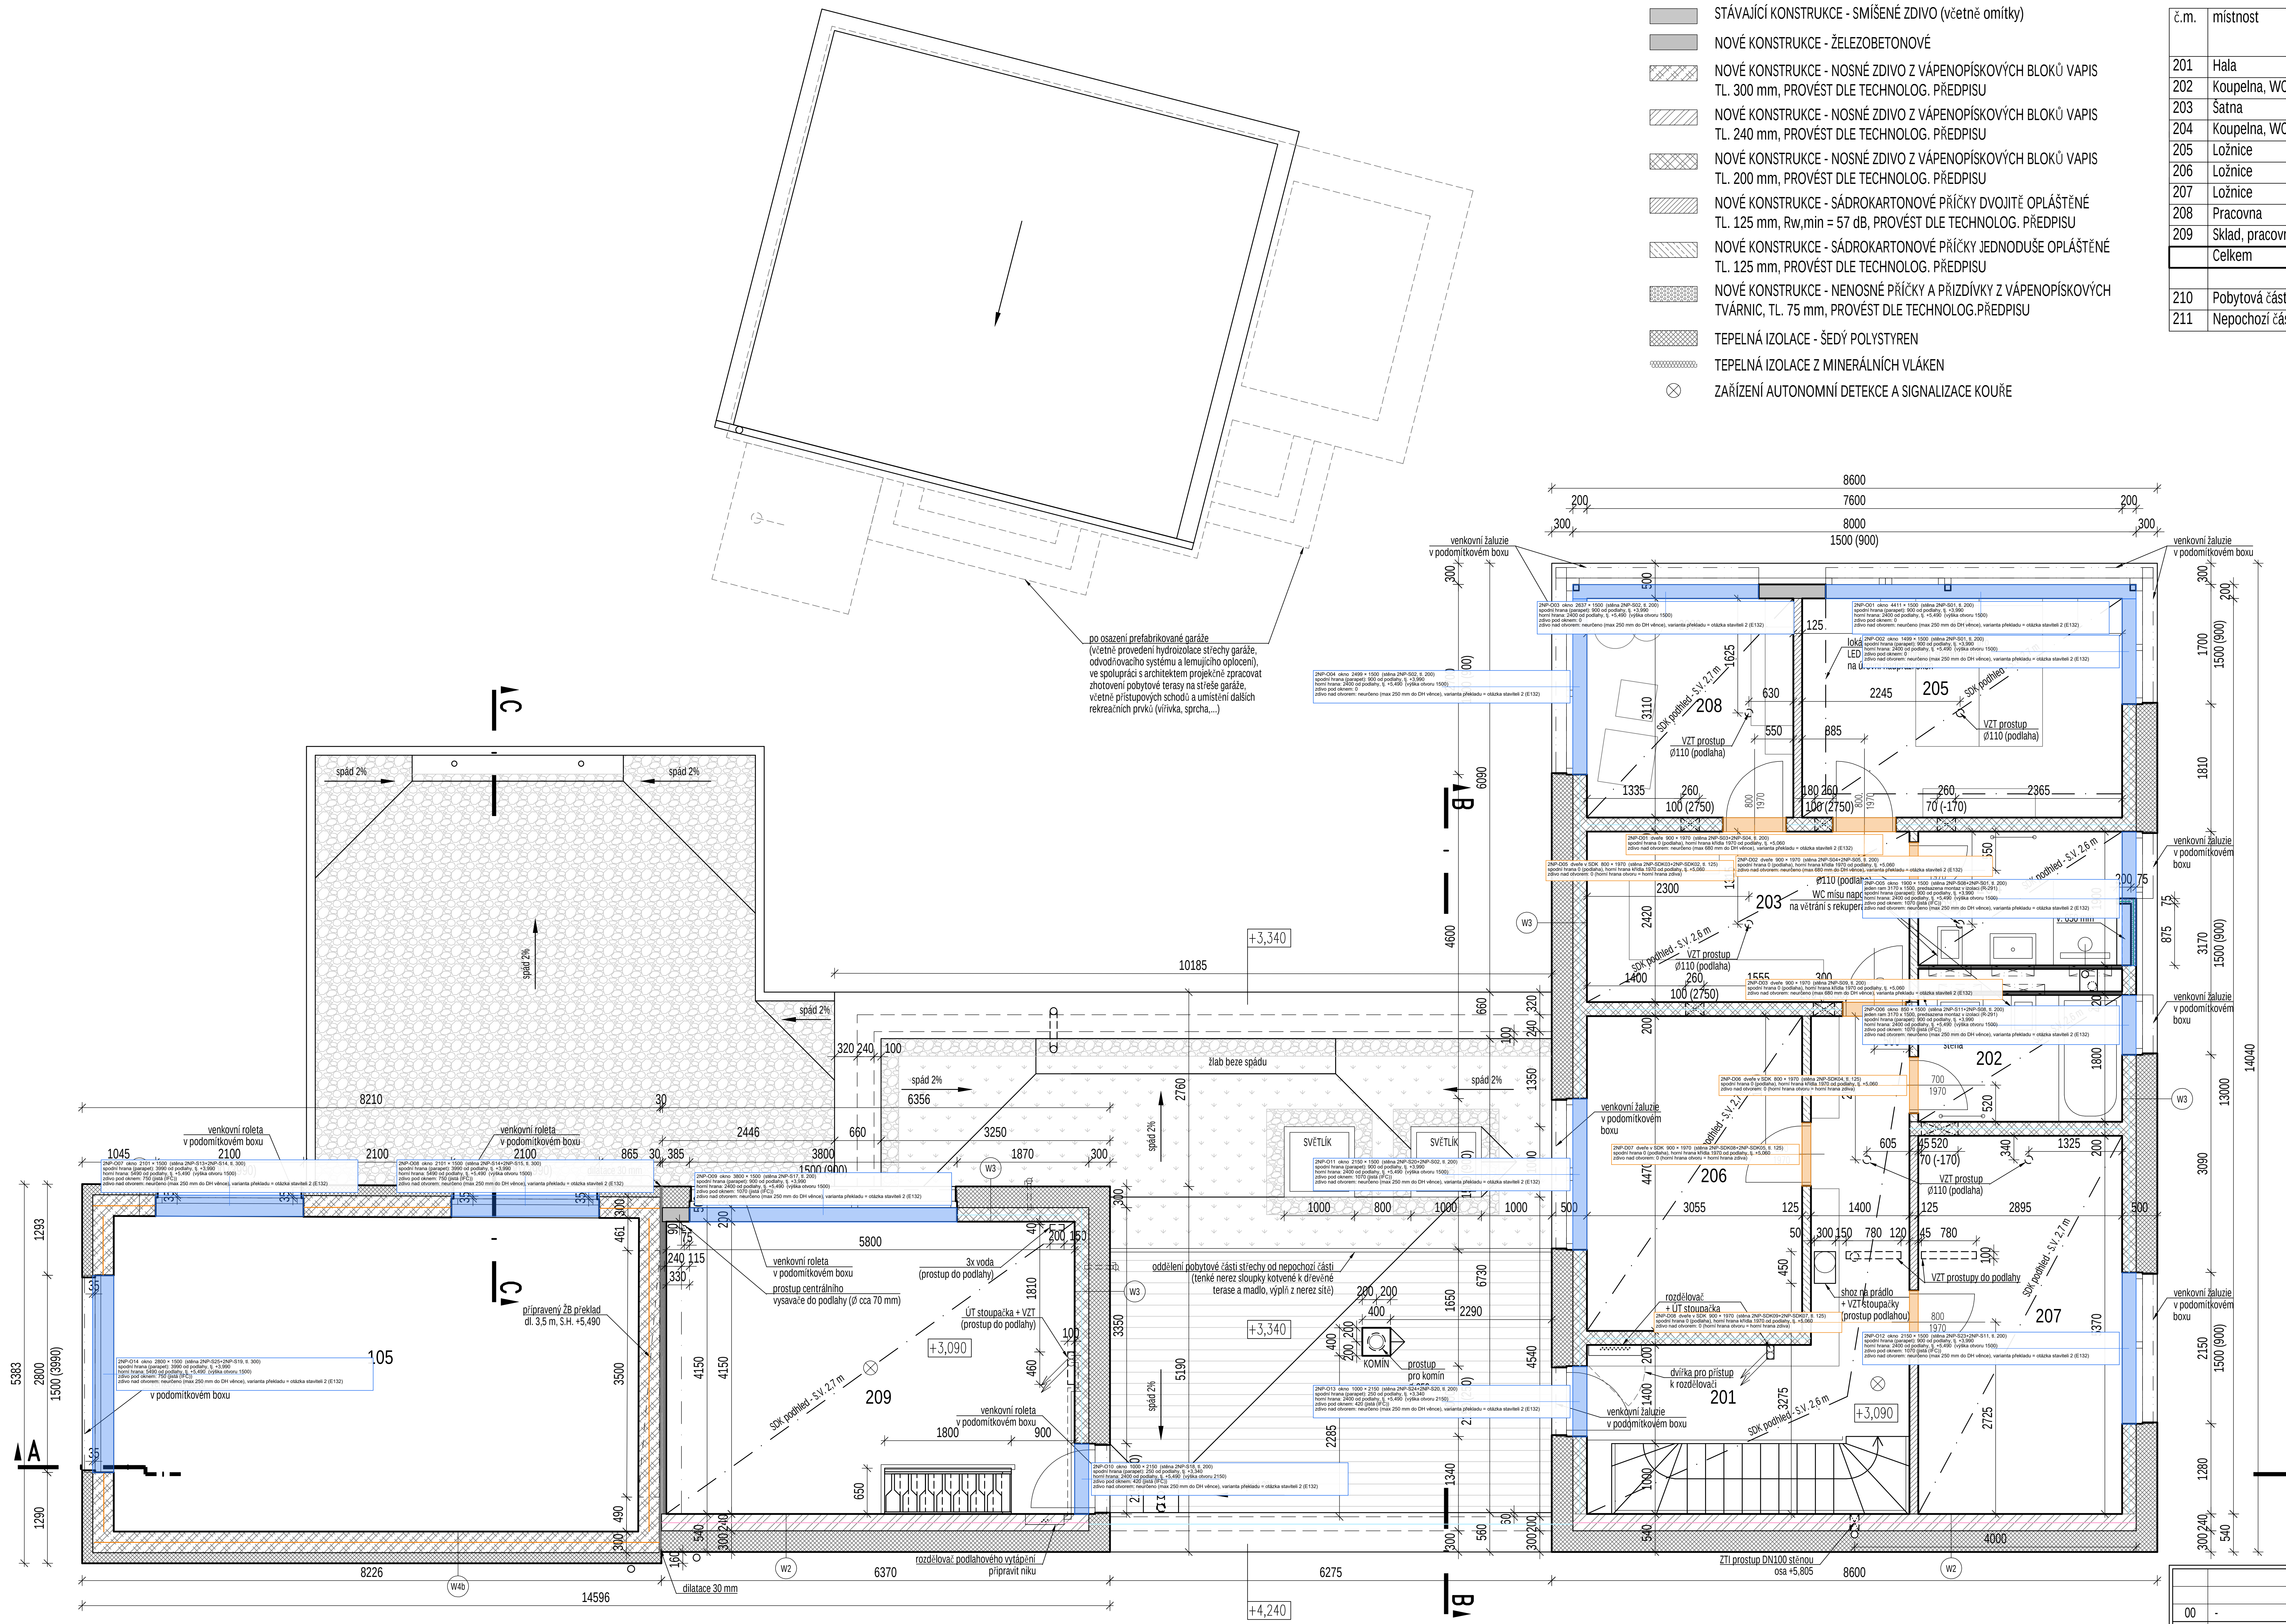
po osazení prefabrikované garáže
(včetně provedení hydroizolace střechy garáže, odvodňovacího systému a lemujícího oplocení), ve spolupráci s architektem projekčně zpracovat zhotovení pobytové terasy na střeše garáže, včetně přístupových schodů a umístění dalších rekreačních prvků (vířivka, sprcha,...)
spád 2%
žlab beze spádu
SVĚTLÍK
SVĚTLÍK
+3,340
+3,090
+4,240
oddělení pobytové části střechy od nepochozí části (tenké nerez sloupky kotvené k dřevěné terase a madlo, výplň z nerez sítě)
KOMÍN
prostup pro komín
venkovní roleta v podomítkovém boxu
venkovní žaluzie v podomítkovém boxu
připravený ŽB překlad dl. 3,5 m, S.H. +5,490
prostup centrálního vysavače do podlahy (Ø cca 70 mm)
3x voda (prostup do podlahy)
ÚT stoupačka + VZT (prostup do podlahy)
rozdělovač podlahového vytápění připravit niku
dilatace 30 mm
SDK podhled - S.V. 2,7 m
SDK podhled - S.V. 2,6 m
VZT prostup Ø110 (podlaha)
VZT prostupy do podlahy
WC mísu napojit na větrání s rekuperací
lokální LED osvětlení na úrovni nadpraží oken
shoz na prádlo + VZT stoupačky (prostup podlahou)
rozdělovač + ÚT stoupačka
dvířka pro přístup k rozdělovači
ZTI prostup DN100 stěnou osa +5,805
105
201
202
203
204
205
206
207
208
209
W2
W3
W4b
A
B
C
2NP-O01 okno 4411 × 1500 (stěna 2NP-S01, tl. 200) spodní hrana (parapet): 900 od podlahy, tj. +3,990 horní hrana: 2400 od podlahy, tj. +5,490 (výška otvoru 1500) zdivo pod oknem: 0 zdivo nad otvorem: neurčeno (max 250 mm do DH věnce), varianta překladu = otázka staviteli 2 (E132)
2NP-O02 okno 1499 × 1500 (stěna 2NP-S01, tl. 200) spodní hrana (parapet): 900 od podlahy, tj. +3,990 horní hrana: 2400 od podlahy, tj. +5,490 (výška otvoru 1500) zdivo pod oknem: 0 zdivo nad otvorem: neurčeno (max 250 mm do DH věnce), varianta překladu = otázka staviteli 2 (E132)
2NP-O03 okno 2637 × 1500 (stěna 2NP-S02, tl. 200) spodní hrana (parapet): 900 od podlahy, tj. +3,990 horní hrana: 2400 od podlahy, tj. +5,490 (výška otvoru 1500) zdivo pod oknem: 0 zdivo nad otvorem: neurčeno (max 250 mm do DH věnce), varianta překladu = otázka staviteli 2 (E132)
2NP-O04 okno 2499 × 1500 (stěna 2NP-S02, tl. 200) spodní hrana (parapet): 900 od podlahy, tj. +3,990 horní hrana: 2400 od podlahy, tj. +5,490 (výška otvoru 1500) zdivo pod oknem: 0 zdivo nad otvorem: neurčeno (max 250 mm do DH věnce), varianta překladu = otázka staviteli 2 (E132)
2NP-O05 okno 1900 × 1500 (stěna 2NP-S08+2NP-S01, tl. 200) jeden ram 3170 x 1500, predsazena montaz v izolaci (R-291) spodní hrana (parapet): 900 od podlahy, tj. +3,990 horní hrana: 2400 od podlahy, tj. +5,490 (výška otvoru 1500) zdivo pod oknem: 1070 (jistá (IFC)) zdivo nad otvorem: neurčeno (max 250 mm do DH věnce), varianta překladu = otázka staviteli 2 (E132)
2NP-O06 okno 850 × 1500 (stěna 2NP-S11+2NP-S08, tl. 200) jeden ram 3170 x 1500, predsazena montaz v izolaci (R-291) spodní hrana (parapet): 900 od podlahy, tj. +3,990 horní hrana: 2400 od podlahy, tj. +5,490 (výška otvoru 1500) zdivo pod oknem: 1070 (jistá (IFC)) zdivo nad otvorem: neurčeno (max 250 mm do DH věnce), varianta překladu = otázka staviteli 2 (E132)
2NP-O07 okno 2101 × 1500 (stěna 2NP-S13+2NP-S14, tl. 300) spodní hrana (parapet): 3990 od podlahy, tj. +3,990 horní hrana: 5490 od podlahy, tj. +5,490 (výška otvoru 1500) zdivo pod oknem: 750 (jistá (IFC)) zdivo nad otvorem: neurčeno (max 250 mm do DH věnce), varianta překladu = otázka staviteli 2 (E132)
2NP-O08 okno 2101 × 1500 (stěna 2NP-S14+2NP-S15, tl. 300) spodní hrana (parapet): 3990 od podlahy, tj. +3,990 horní hrana: 5490 od podlahy, tj. +5,490 (výška otvoru 1500) zdivo pod oknem: 750 (jistá (IFC)) zdivo nad otvorem: neurčeno (max 250 mm do DH věnce), varianta překladu = otázka staviteli 2 (E132)
2NP-O09 okno 3800 × 1500 (stěna 2NP-S17, tl. 200) spodní hrana (parapet): 900 od podlahy, tj. +3,990 horní hrana: 2400 od podlahy, tj. +5,490 (výška otvoru 1500) zdivo pod oknem: 1070 (jistá (IFC)) zdivo nad otvorem: neurčeno (max 250 mm do DH věnce), varianta překladu = otázka staviteli 2 (E132)
2NP-O10 okno 1000 × 2150 (stěna 2NP-S18, tl. 200) spodní hrana (parapet): 250 od podlahy, tj. +3,340 horní hrana: 2400 od podlahy, tj. +5,490 (výška otvoru 2150) zdivo pod oknem: 420 (jistá (IFC)) zdivo nad otvorem: neurčeno (max 250 mm do DH věnce), varianta překladu = otázka staviteli 2 (E132)
2NP-O11 okno 2150 × 1500 (stěna 2NP-S20+2NP-S02, tl. 200) spodní hrana (parapet): 900 od podlahy, tj. +3,990 horní hrana: 2400 od podlahy, tj. +5,490 (výška otvoru 1500) zdivo pod oknem: 1070 (jistá (IFC)) zdivo nad otvorem: neurčeno (max 250 mm do DH věnce), varianta překladu = otázka staviteli 2 (E132)
2NP-O12 okno 2150 × 1500 (stěna 2NP-S23+2NP-S11, tl. 200) spodní hrana (parapet): 900 od podlahy, tj. +3,990 horní hrana: 2400 od podlahy, tj. +5,490 (výška otvoru 1500) zdivo pod oknem: 1070 (jistá (IFC)) zdivo nad otvorem: neurčeno (max 250 mm do DH věnce), varianta překladu = otázka staviteli 2 (E132)
2NP-O13 okno 1000 × 2150 (stěna 2NP-S24+2NP-S20, tl. 200) spodní hrana (parapet): 250 od podlahy, tj. +3,340 horní hrana: 2400 od podlahy, tj. +5,490 (výška otvoru 2150) zdivo pod oknem: 420 (jistá (IFC)) zdivo nad otvorem: neurčeno (max 250 mm do DH věnce), varianta překladu = otázka staviteli 2 (E132)
2NP-O14 okno 2800 × 1500 (stěna 2NP-S25+2NP-S19, tl. 300) spodní hrana (parapet): 3990 od podlahy, tj. +3,990 horní hrana: 5490 od podlahy, tj. +5,490 (výška otvoru 1500) zdivo pod oknem: 750 (jistá (IFC)) zdivo nad otvorem: neurčeno (max 250 mm do DH věnce), varianta překladu = otázka staviteli 2 (E132)
2NP-D01 dveře 900 × 1970 (stěna 2NP-S03+2NP-S04, tl. 200) spodní hrana 0 (podlaha), horní hrana křídla 1970 od podlahy, tj. +5,060 zdivo nad otvorem: neurčeno (max 680 mm do DH věnce), varianta překladu = otázka staviteli 2 (E132)
2NP-D02 dveře 900 × 1970 (stěna 2NP-S04+2NP-S05, tl. 200) spodní hrana 0 (podlaha), horní hrana křídla 1970 od podlahy, tj. +5,060 zdivo nad otvorem: neurčeno (max 680 mm do DH věnce), varianta překladu = otázka staviteli 2 (E132)
2NP-D03 dveře 900 × 1970 (stěna 2NP-S09, tl. 200) spodní hrana 0 (podlaha), horní hrana křídla 1970 od podlahy, tj. +5,060 zdivo nad otvorem: neurčeno (max 680 mm do DH věnce), varianta překladu = otázka staviteli 2 (E132)
2NP-D05 dveře v SDK 800 × 1970 (stěna 2NP-SDK03+2NP-SDK02, tl. 125) spodní hrana 0 (podlaha), horní hrana křídla 1970 od podlahy, tj. +5,060 zdivo nad otvorem: 0 (horní hrana otvoru = horní hrana zdiva)
2NP-D06 dveře v SDK 800 × 1970 (stěna 2NP-SDK04, tl. 125) spodní hrana 0 (podlaha), horní hrana křídla 1970 od podlahy, tj. +5,060 zdivo nad otvorem: 0 (horní hrana otvoru = horní hrana zdiva)
2NP-D07 dveře v SDK 900 × 1970 (stěna 2NP-SDK08+2NP-SDK05, tl. 125) spodní hrana 0 (podlaha), horní hrana křídla 1970 od podlahy, tj. +5,060 zdivo nad otvorem: 0 (horní hrana otvoru = horní hrana zdiva)
2NP-D08 dveře v SDK 900 × 1970 (stěna 2NP-SDK09+2NP-SDK07, tl. 125) spodní hrana 0 (podlaha), horní hrana křídla 1970 od podlahy, tj. +5,060 zdivo nad otvorem: 0 (horní hrana otvoru = horní hrana zdiva)
8600
7600
8000
1500 (900)
10185
8210
14596
8226
6370
6275
5383
14040
13000

00	-	-	-
Revize:	Obsah změny:	Autor:	Datum:

Název akce: **NOVOSTAVBA RODINNÉHO DOMU**

Paré:

Místo stavby: adresa stavby neuvedena

Objednatel: investor

Generální projektant:

Profese:

Projektant: projektantka

Projekční tým: projektantka

Kontroloval:

Autorizační razítko:

Formát: -

Měřítko: 1:50

Část: ARCHITEKTONICKO - STAVEBNÍ

Číslo projektu:

Datum: 09/2026

Stupeň: -

Vydal: projektantka

Obsah výkresu: **PŮDORYS 2.NP**

Číslo výkresu: **D11-02**

DOKUMENTACE JE DUSEVNIM MAJETKEM FIRMY RECOC S.R.O. A NESMI BYT POUZITA BEZ JEJIHO VEDOMI