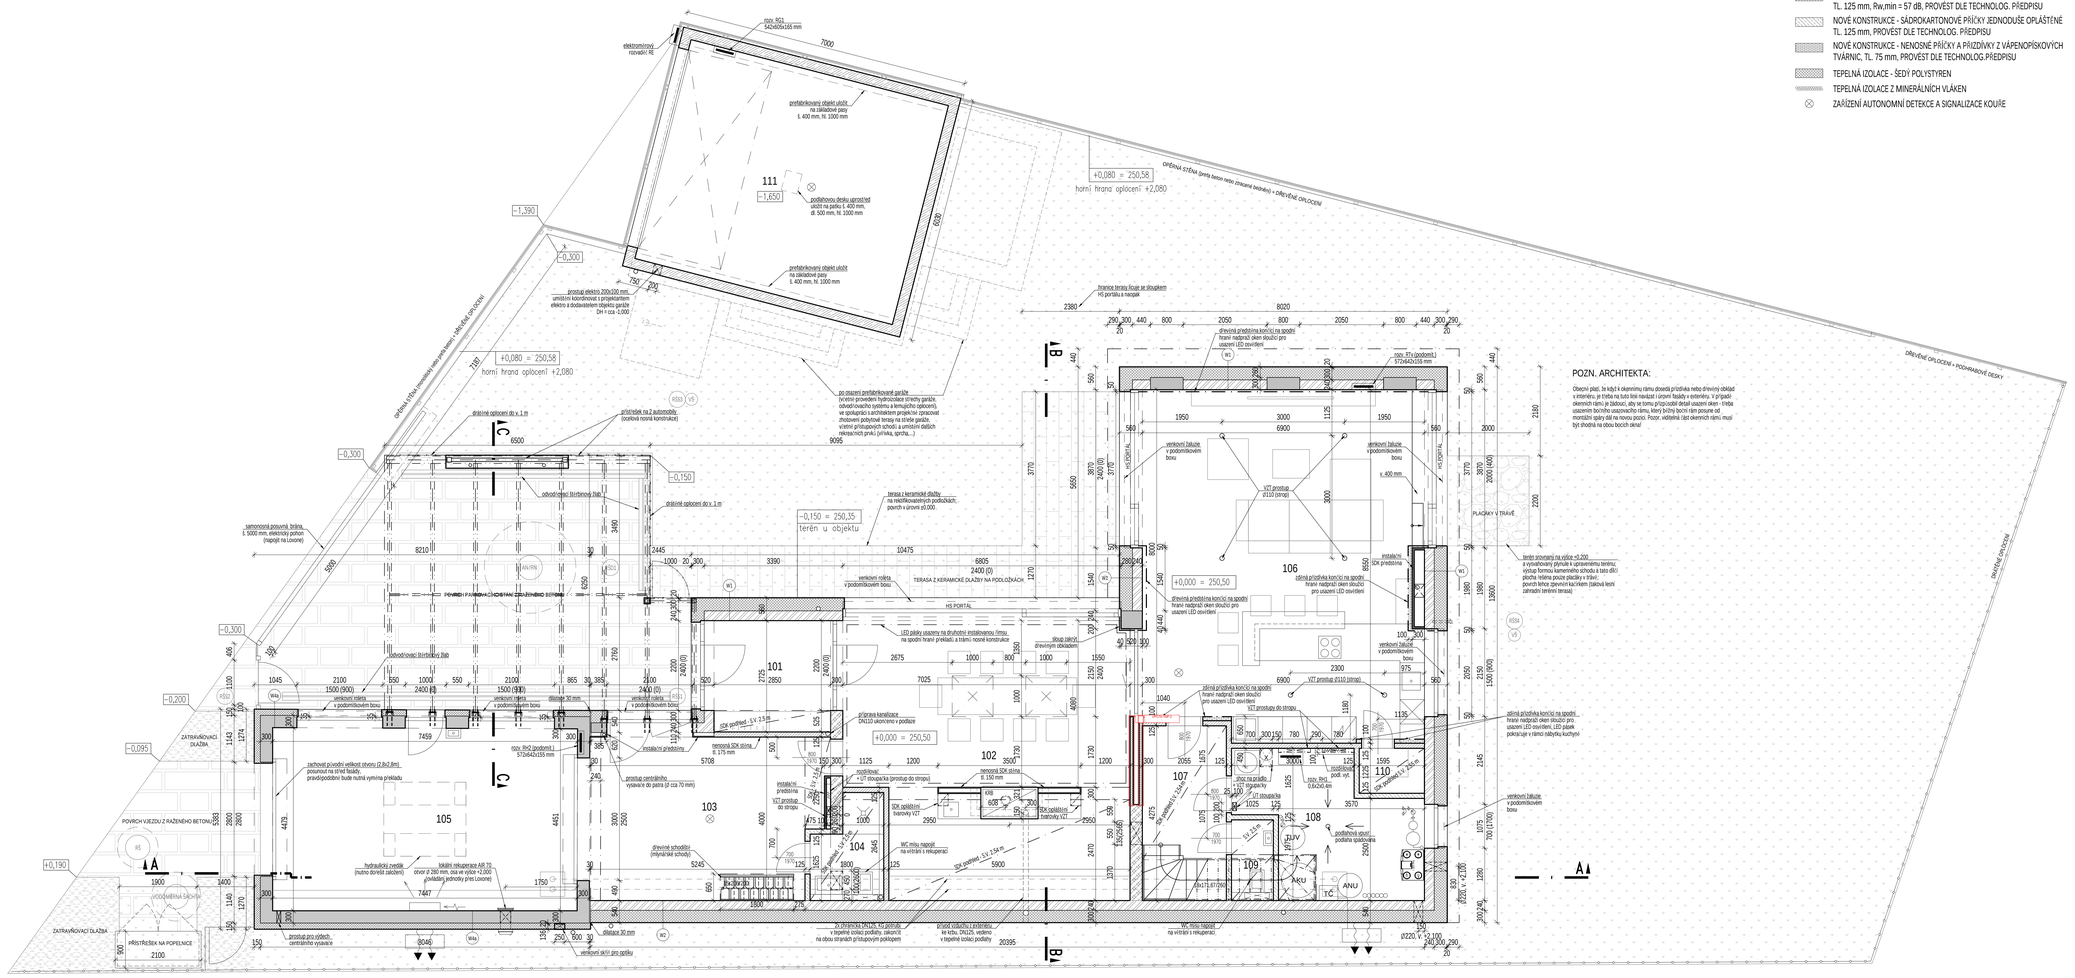
1 MP: line plochy se šrafou VPC 75 (hexido 75 x 2150 mm); mezi 102 a 107


+0,080 = 250,58
horní hrana opláštění +2,080
−1,390
−0,300
−0,150
−0,150 = 250,35
terén u objektu
+0,000 = 250,50
+0,190
111
−1,650
podlahovou desku ukotvit
uložit na patku š. 400 mm,
dl. 500 mm, hl. 1000 mm
prefabrikovaný objekt uložit
na základové pasy
š. 400 mm, hl. 1000 mm
prostup elektro 200x100 mm,
umístění koordinovat s projektantem
elektro a dodavatelem objektu garáže
DH + cca -1,000
po osazení prefabrikované garáže
(vnitřní prostřední hydroizolace stěrky garáže,
odvodňovacího systému a ikmujícího opláštění),
ve spolupráci s architektem projektovat
zhotovení jednotné stěrky na stěnách garáží,
vnitřní přístupových schodů a umístění dalších
konstrukčních prvků (přípěrka, spirála, ...)
9095
6500
7000
6020
750
200
2180
2380
9020
2050
800
440
290
300
20
1950
3000
1125
6900
560
2000
3870
2400 (400)
2200
2400 (0)
5650
3370
3710
2180
venkovní žaluzie
v podomítkovém boxu
VCT prostup
Ø110 (strop)
v. 400 mm
PLACHTY V TRÁVĚ
HS PORTÁL
HS PORTÁL
106
8650
6805
2400 (0)
10475
TERASA Z KERAMICKÉ DLAŽBY NA PODLOŽKÁCH
1270
1540
+0,000 = 250,50
instalační
SDK předstěna
dřevěná předsňna končící na spodní
hraně nadpraží oken slouží pro
uzavření LED osvětlení
dřevěná předsňna končící na spodní
hraně nadpraží oken slouží pro
uzavření LED osvětlení
terén srovnaný na výšce +0,200
a vysahovaný plynule k upravovanému terénu,
výstup formou kamenného schodu a tato dílčí
plocha hrána pouze plackáry v třávě,
povrch lehce zpevnit kačírkem (takovú lesní
zámradní terénní terasa)
LED pásky usazeny na druhotné instalovanou rímsu
na spodní hraně překladu a trámů nosné konstrukce
sloup nárožní
dřevěných obkladem
40
520
300
2675
1000
800
1550
2150
2400
7025
4089
2300
975
560
2055
1500 (900)
1040
1180
1135
1595
110
2145
1100
1000
1550
2400 (0)
2200
2400 (0)
2760
2850
101
2675
1000
800
1000